


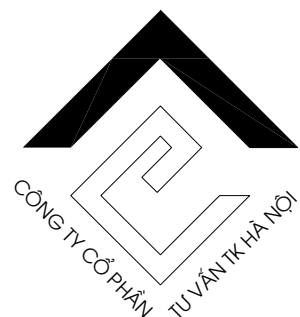


CÔNG TY CỔ PHẦN TƯ VẤN THIẾT KẾ HÀ NỘI

HỒ SƠ XIN PHÉP XÂY DỰNG

HẠNG MỤC : KHÁCH SẠN

CHỦ ĐẦU TƯ : ANH SỸ

ĐỊA ĐIỂM XÂY DỰNG : THÔN YÊN LỆNH, XÃ THÁI THỤY, TỈNH HUNG YÊN

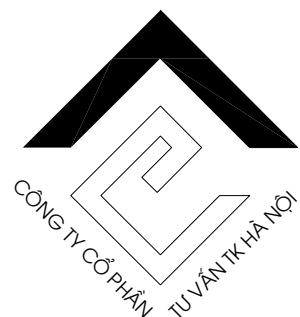

CÔNG TY CỔ PHẦN TƯ VẤN THIẾT KẾ HÀ NỘI

HỒ SƠ XIN PHÉP XÂY DỰNG


HẠNG MỤC : KHÁCH SẠN

CHỦ ĐẦU TƯ : ANH SỸ


ĐỊA ĐIỂM XÂY DỰNG : THÔN YÊN LỆNH, XÃ THÁI THỤY, TỈNH HUNG YÊN

CHỦ ĐẦU TƯ

ĐƠN VỊ TƯ VẤN THIẾT KẾ

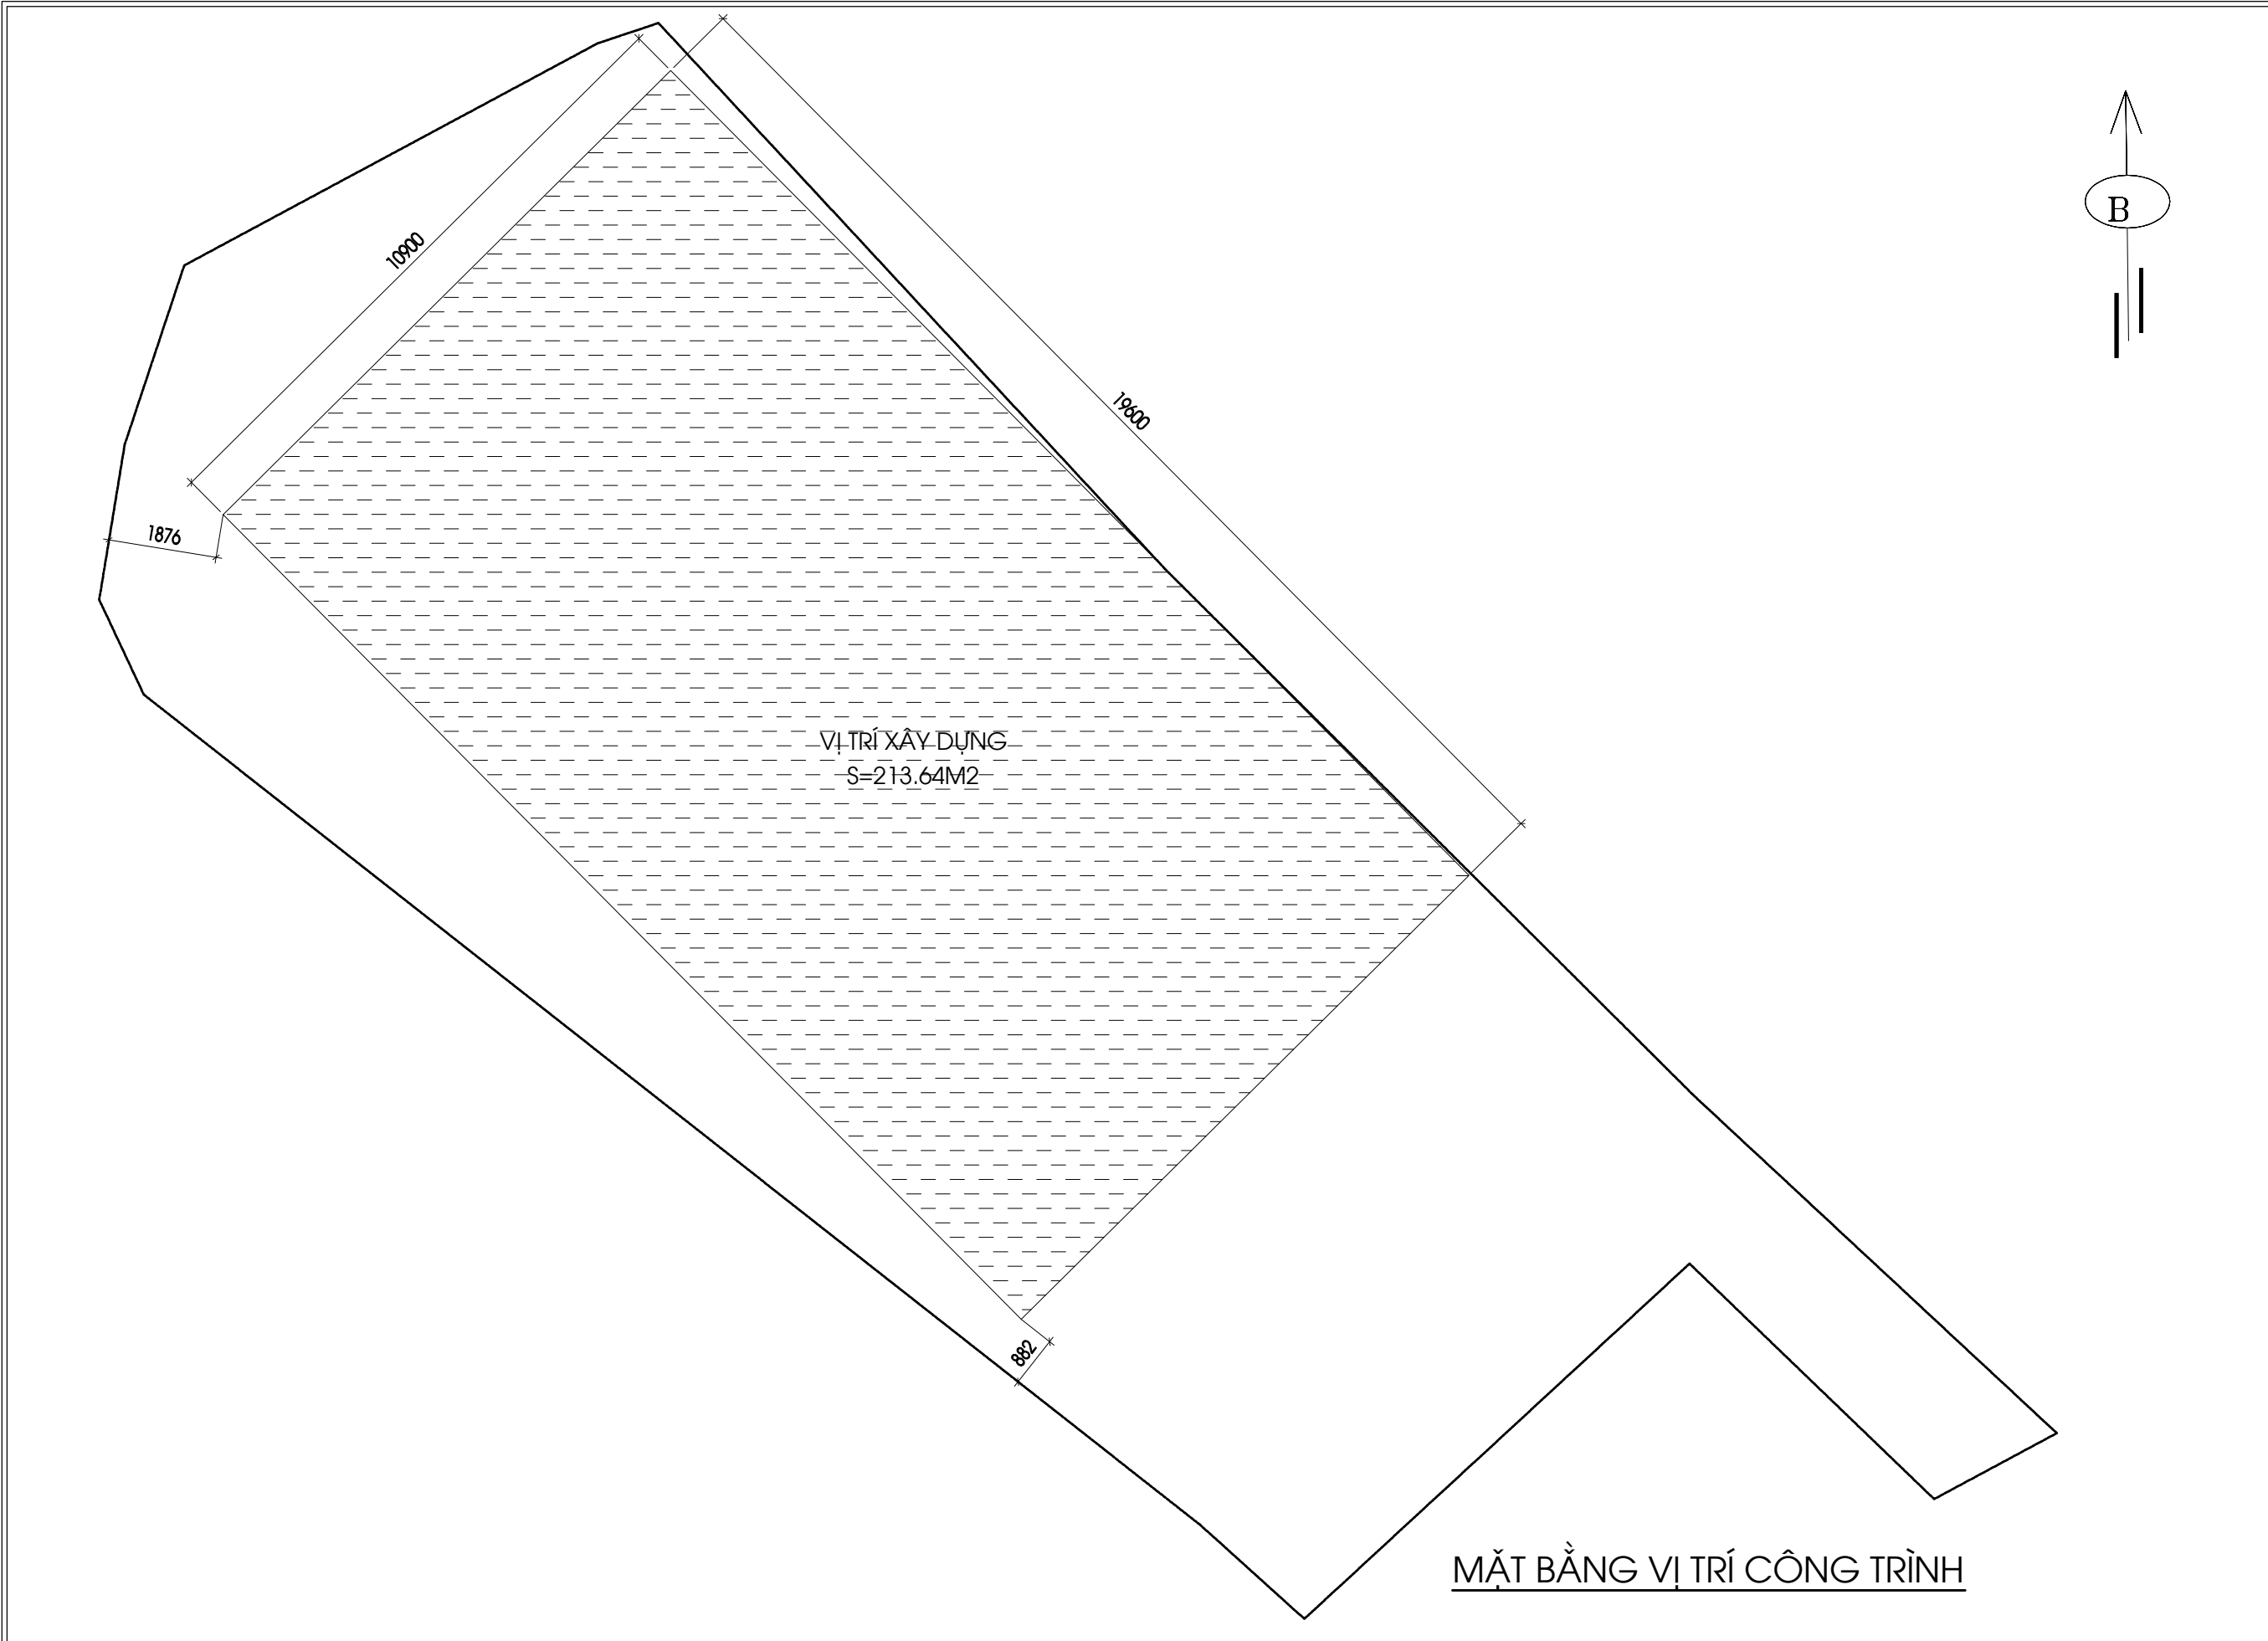

CHỦ ĐẦU TƯ	
ANH SỸ	
CÔNG TRÌNH	
KHÁCH SẠN	
ĐỊA ĐIỂM	
YÊN LỆNH, THÁI THUY, HUNG YÊN	
ĐƠN VỊ THIẾT KẾ	
CÔNG TY CỔ PHẦN TƯ VẤN THIẾT KẾ NHÀ ĐẸP ĐC: SN71 SƠN ĐỒNG, HÀ NỘI TEL: 0983.381.930	
GIÁM ĐỐC	
NGUYỄN ĐỨC MINH	
CHỦ TRÌ DỰ ÁN	
KTS. NGUYỄN ĐỨC MINH	
THIẾT KẾ	
KTS. NGUYỄN ĐOÀN HIẾU	
KẾT CẤU	
KS. TRẦN VĂN ANH	
GIAI ĐOẠN	H.S.X.P
HẠNG MỤC	
KIẾN TRÚC	
TÊN BẢN VẼ	
MẶT BẰNG VỊ TRÍ CÔNG TRÌNH	
HOÀN THÀNH	02/2026
KÝ HIỆU BẢN VẼ	KT-00

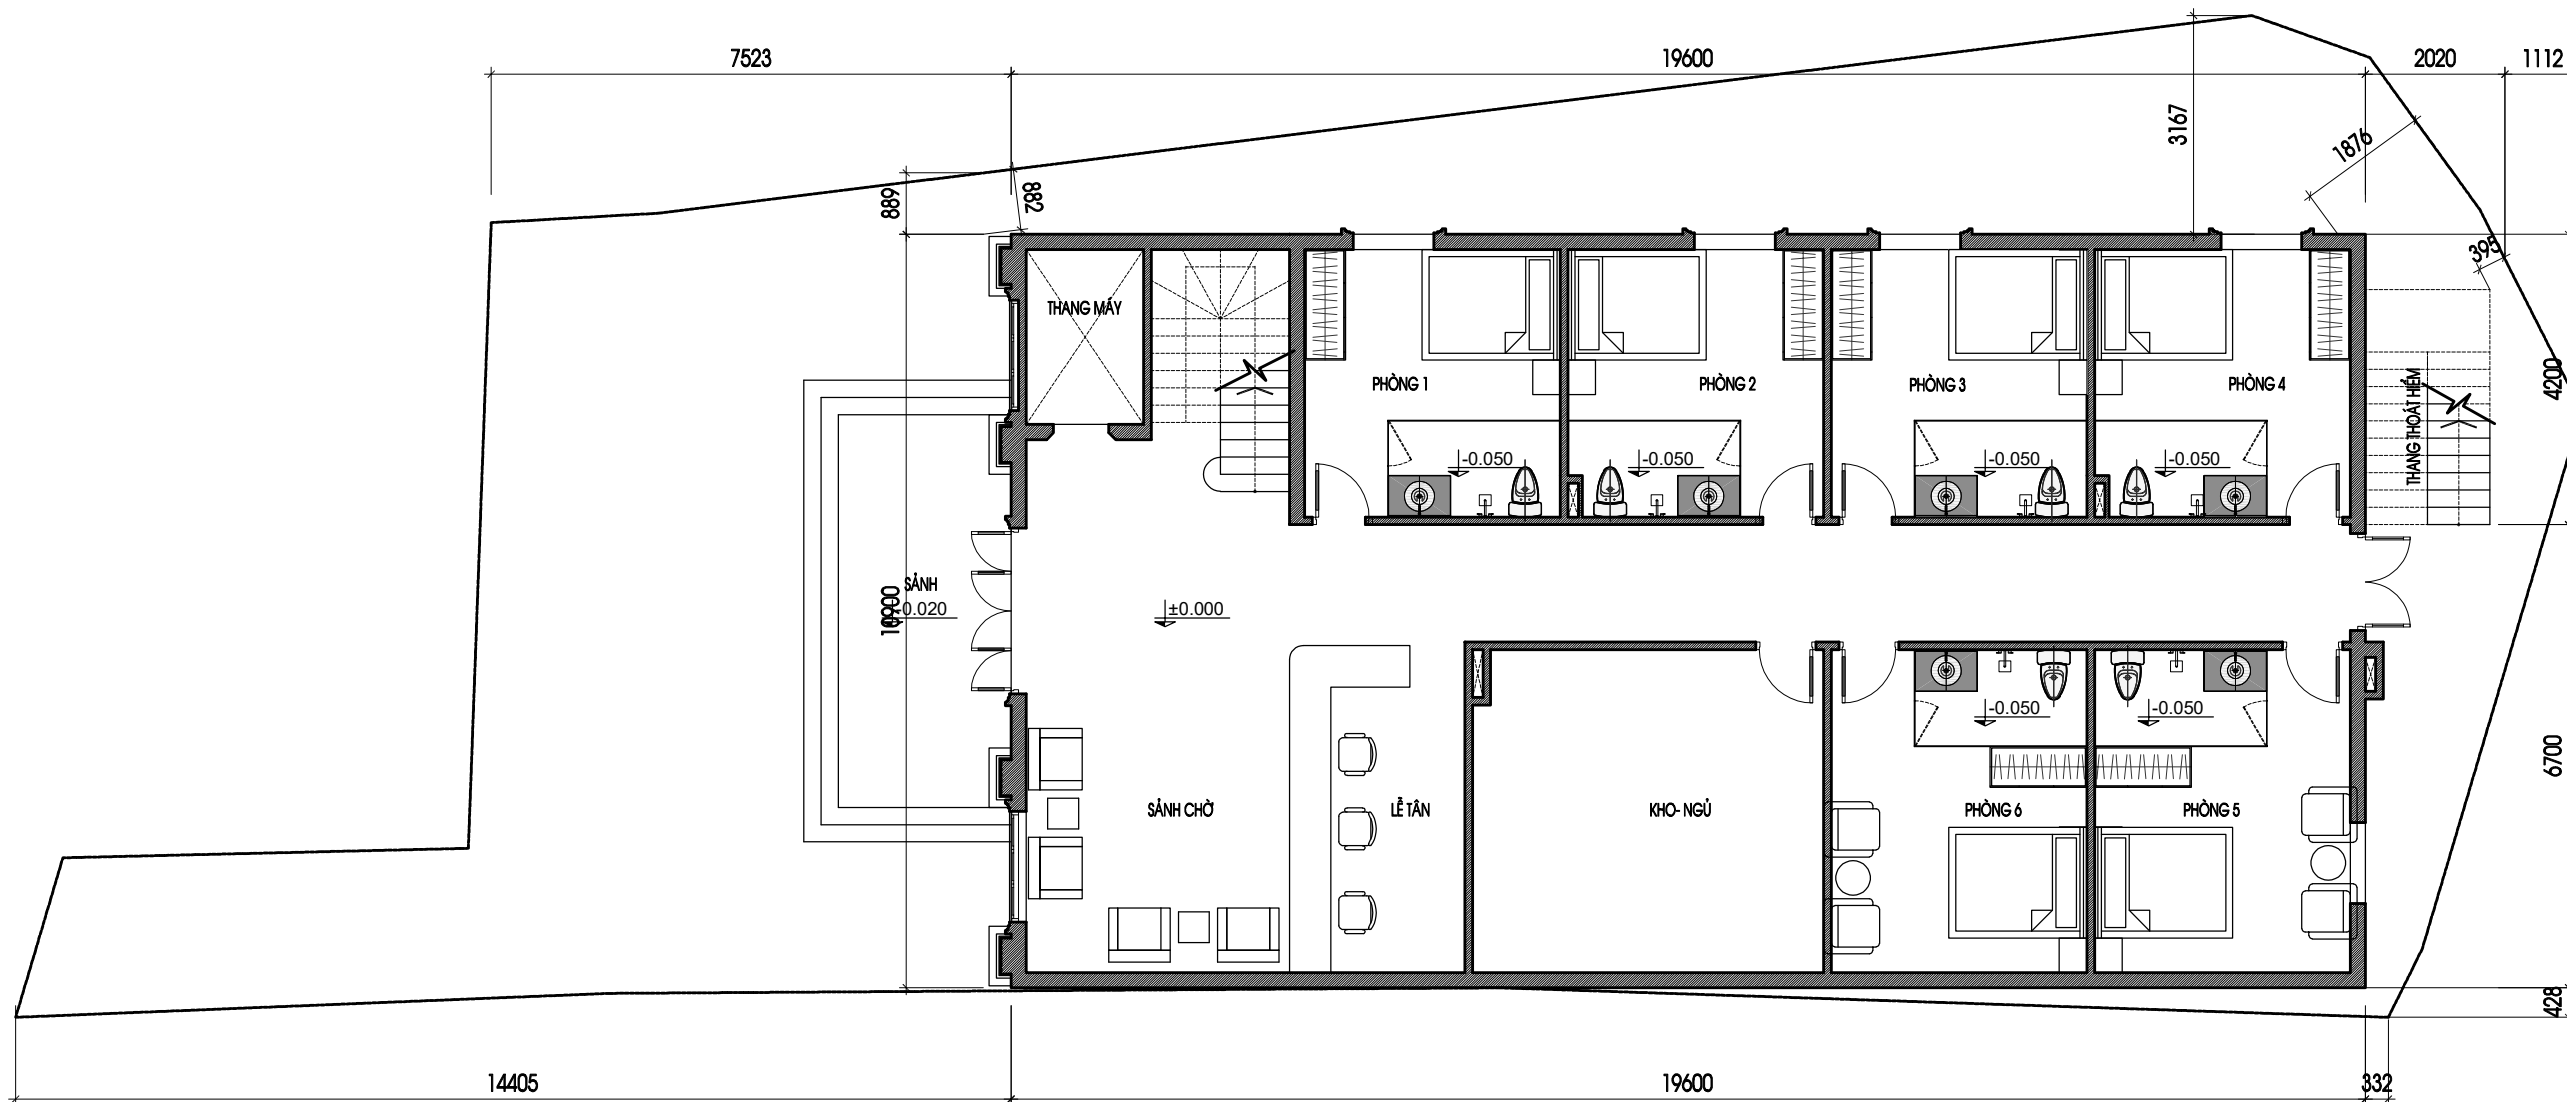

MẶT BẰNG TỔNG THỂ

CHỦ ĐẦU TƯ

ANH SỸ

CÔNG TRÌNH

KHÁCH SẠN

ĐỊA ĐIỂM

YÊN LỆNH, THÁI THUY, HUNG YÊN

ĐƠN VỊ THIẾT KẾ



CÔNG TY CỔ PHẦN
TƯ VẤN THIẾT KẾ HÀ NỘI

ĐC: SN71 SƠN ĐỒNG, HÀ NỘI
TEL: 0983.381.930

GIÁM ĐỐC

(Signature)

NGUYỄN ĐỨC MINH

CHỦ TRÌ DỰ ÁN

(Signature)

KTS. NGUYỄN ĐỨC MINH

THIẾT KẾ

(Signature)

KTS. NGUYỄN DOÀN HIẾU

KẾT CẤU

(Signature)

KS. TRẦN VĂN ANH

GIAI ĐOẠN

H.S.X.P

HẠNG MỤC

KIẾN TRÚC

TÊN BẢN VẼ

MẶT BẰNG TỔNG THỂ

HOÀN THÀNH

02/2026

KÝ HIỆU BẢN VẼ

KT-01



MẶT BẰNG TẦNG 1

CHỦ ĐẦU TƯ

ANH SỸ

CÔNG TRÌNH

KHÁCH SẠN

ĐỊA ĐIỂM

YÊN LỆNH, THÁI THUY, HUNG YÊN

ĐƠN VỊ THIẾT KẾ



CÔNG TY CỔ PHẦN
TƯ VẤN THIẾT KẾ HÀ NỘI

ĐC: SN71 SƠN ĐỒNG, HÀ NỘI
TEL: 0983.381.930

GIÁM ĐỐC

(Signature)

NGUYỄN ĐỨC MINH

CHỦ TRÌ DỰ ÁN

(Signature)

KTS. NGUYỄN ĐỨC MINH

THIẾT KẾ

(Signature)

KTS. NGUYỄN DOÀN HIẾU

KẾT CẤU

(Signature)

KS. TRẦN VĂN ANH

GIẢI ĐOẠN

H.S.X.P

HẠNG MỤC

KIẾN TRÚC

TÊN BẢN VẼ


MẶT BẰNG TẦNG 1

HOÀN THÀNH

02/2026

KÝ HIỆU BẢN VẼ

KT-02

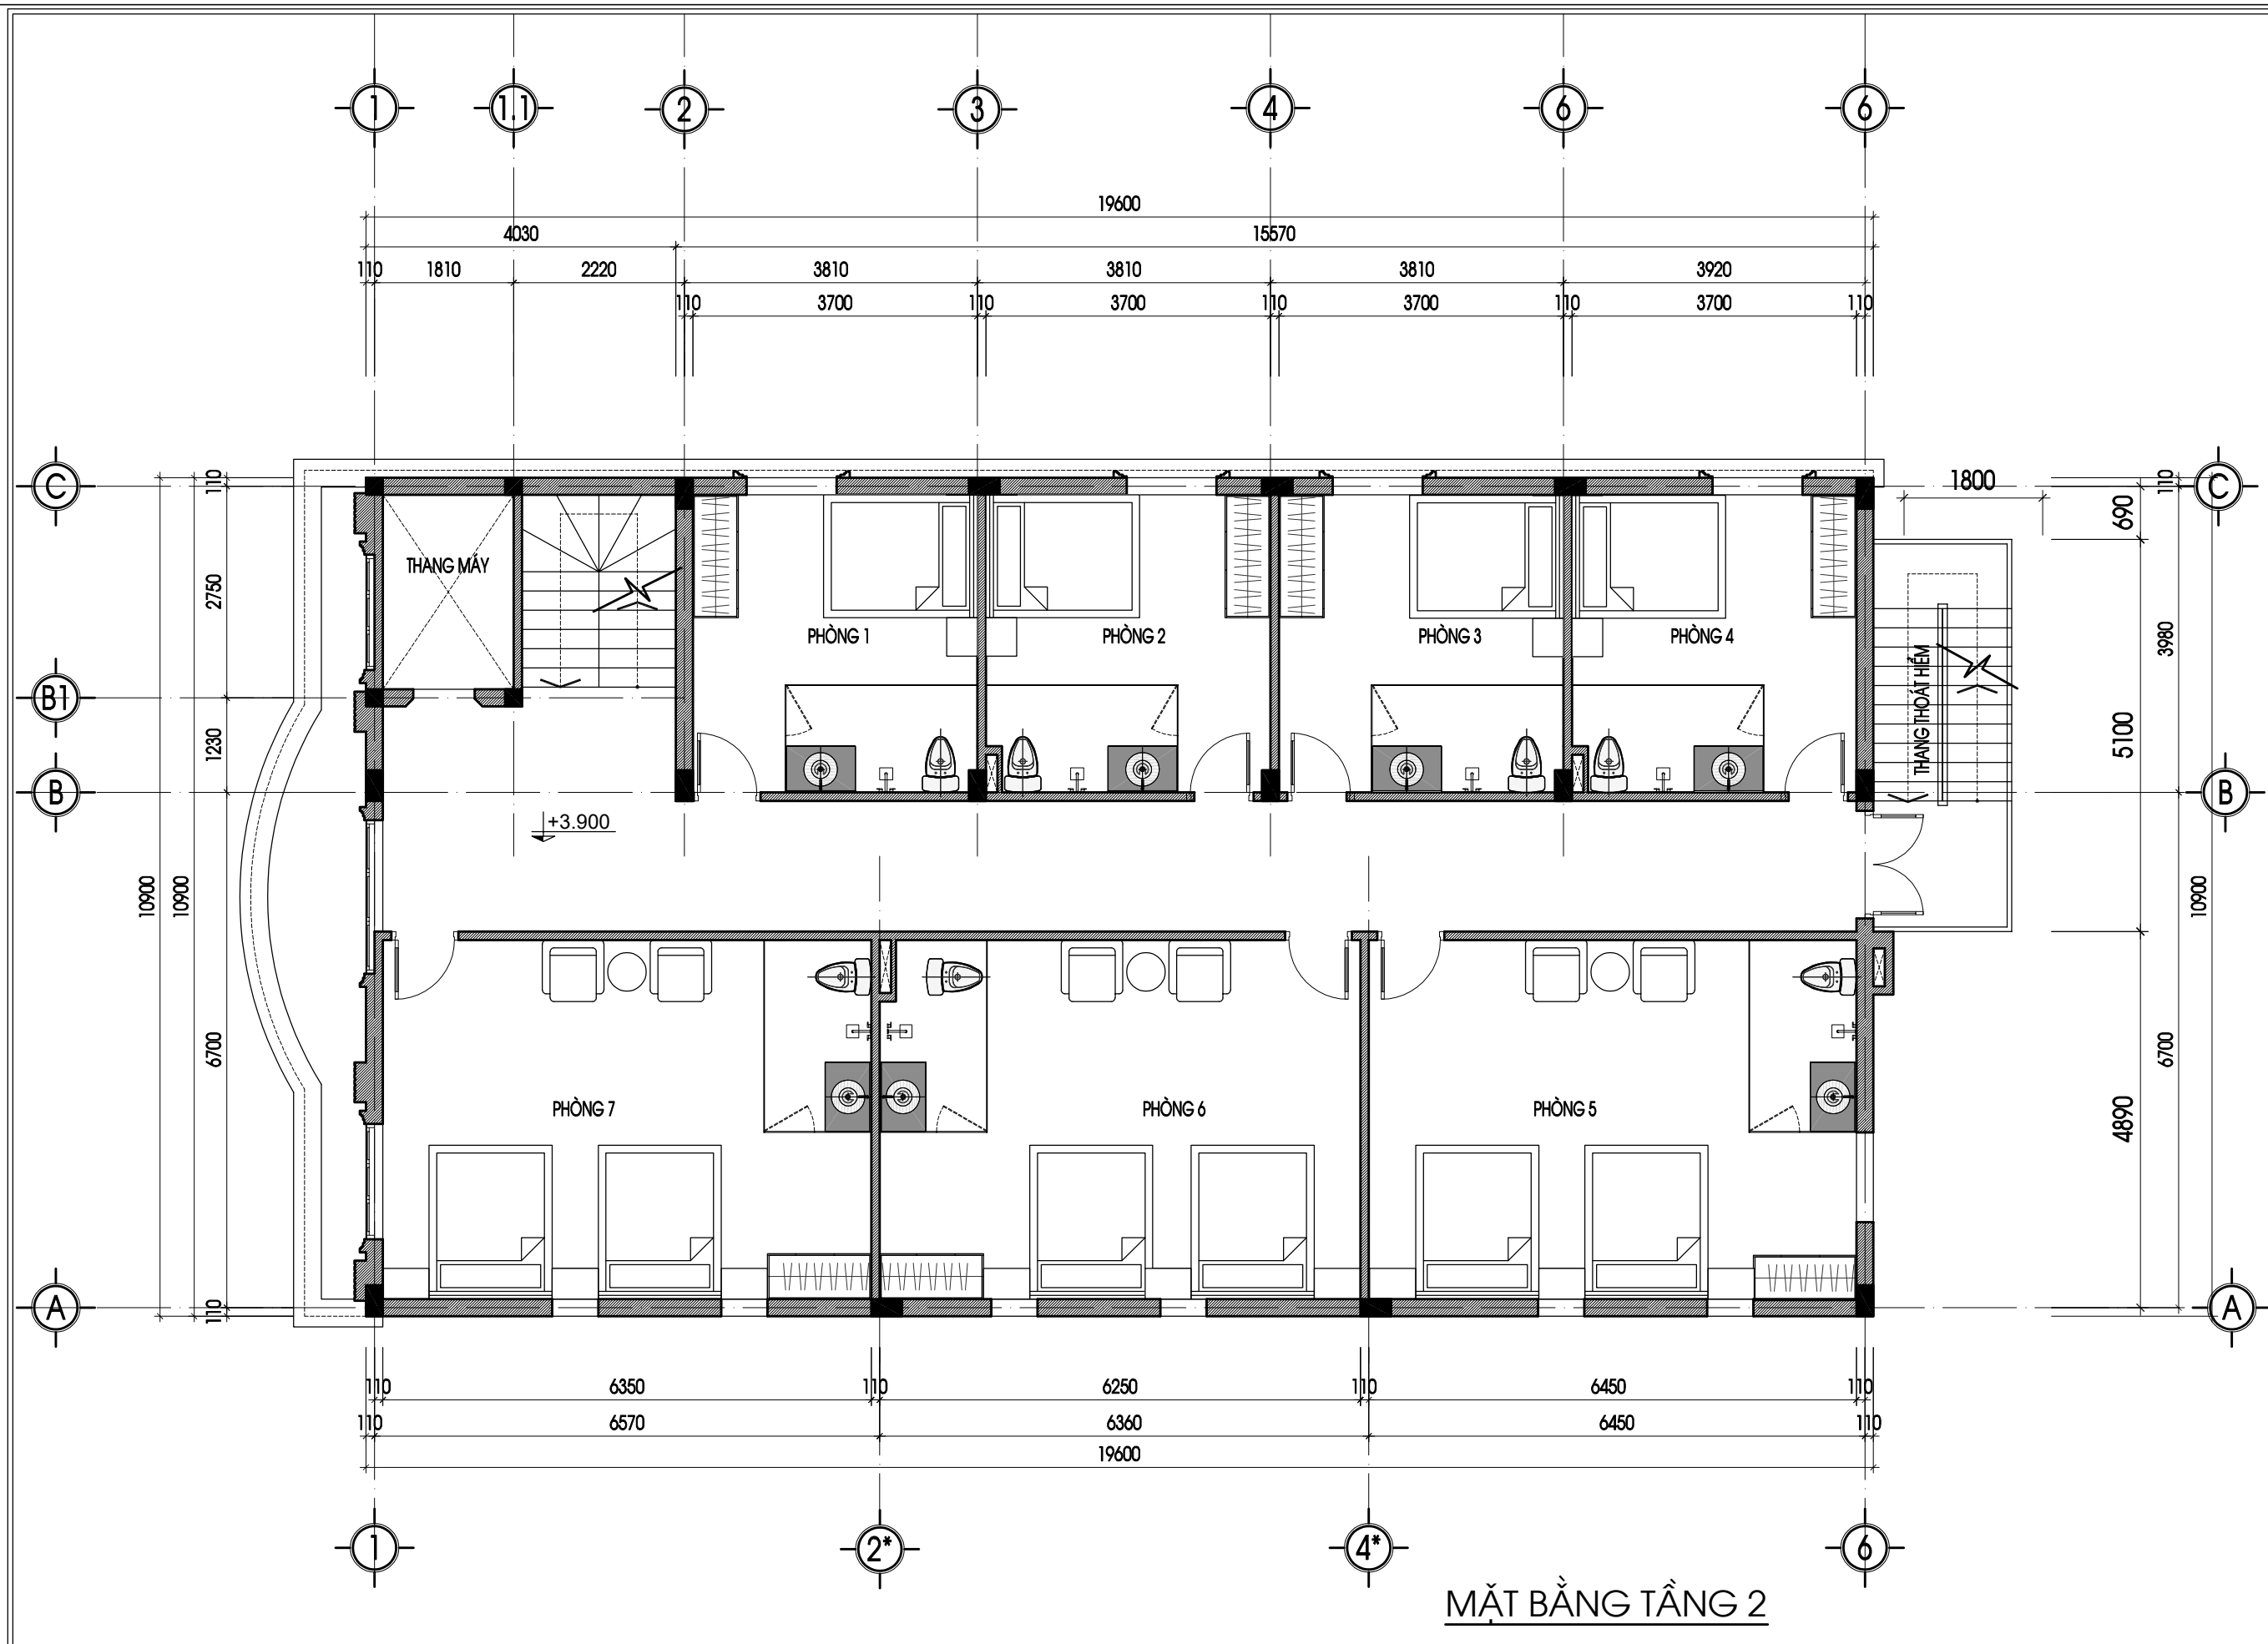

MẶT BẰNG TẦNG 2

CHỦ ĐẦU TƯ

ANH SỸ

CÔNG TRÌNH

KHÁCH SẠN

ĐỊA ĐIỂM

YÊN LỆNH, THÁI THUY, HUNG YÊN

ĐƠN VỊ THIẾT KẾ



CÔNG TY CỔ PHẦN
TƯ VẤN THIẾT KẾ HÀ NỘI
ĐC: SN71 SƠN ĐỒNG, HÀ NỘI
TEL: 0983.381.930

GIÁM ĐỐC

(Signature)

NGUYỄN ĐỨC MINH

CHỦ TRÌ DỰ ÁN

(Signature)

KTS. NGUYỄN ĐỨC MINH

THIẾT KẾ

(Signature)

KTS. NGUYỄN DOÀN HIẾU

KẾT CẤU

(Signature)

KS. TRẦN VĂN ANH

GIẢI ĐOẠN

H.S.X.P

HẠNG MỤC

KIẾN TRÚC

TÊN BẢN VẼ


MẶT BẰNG TẦNG 2

HOÀN THÀNH

02/2026

KÝ HIỆU BẢN VẼ

KT-03

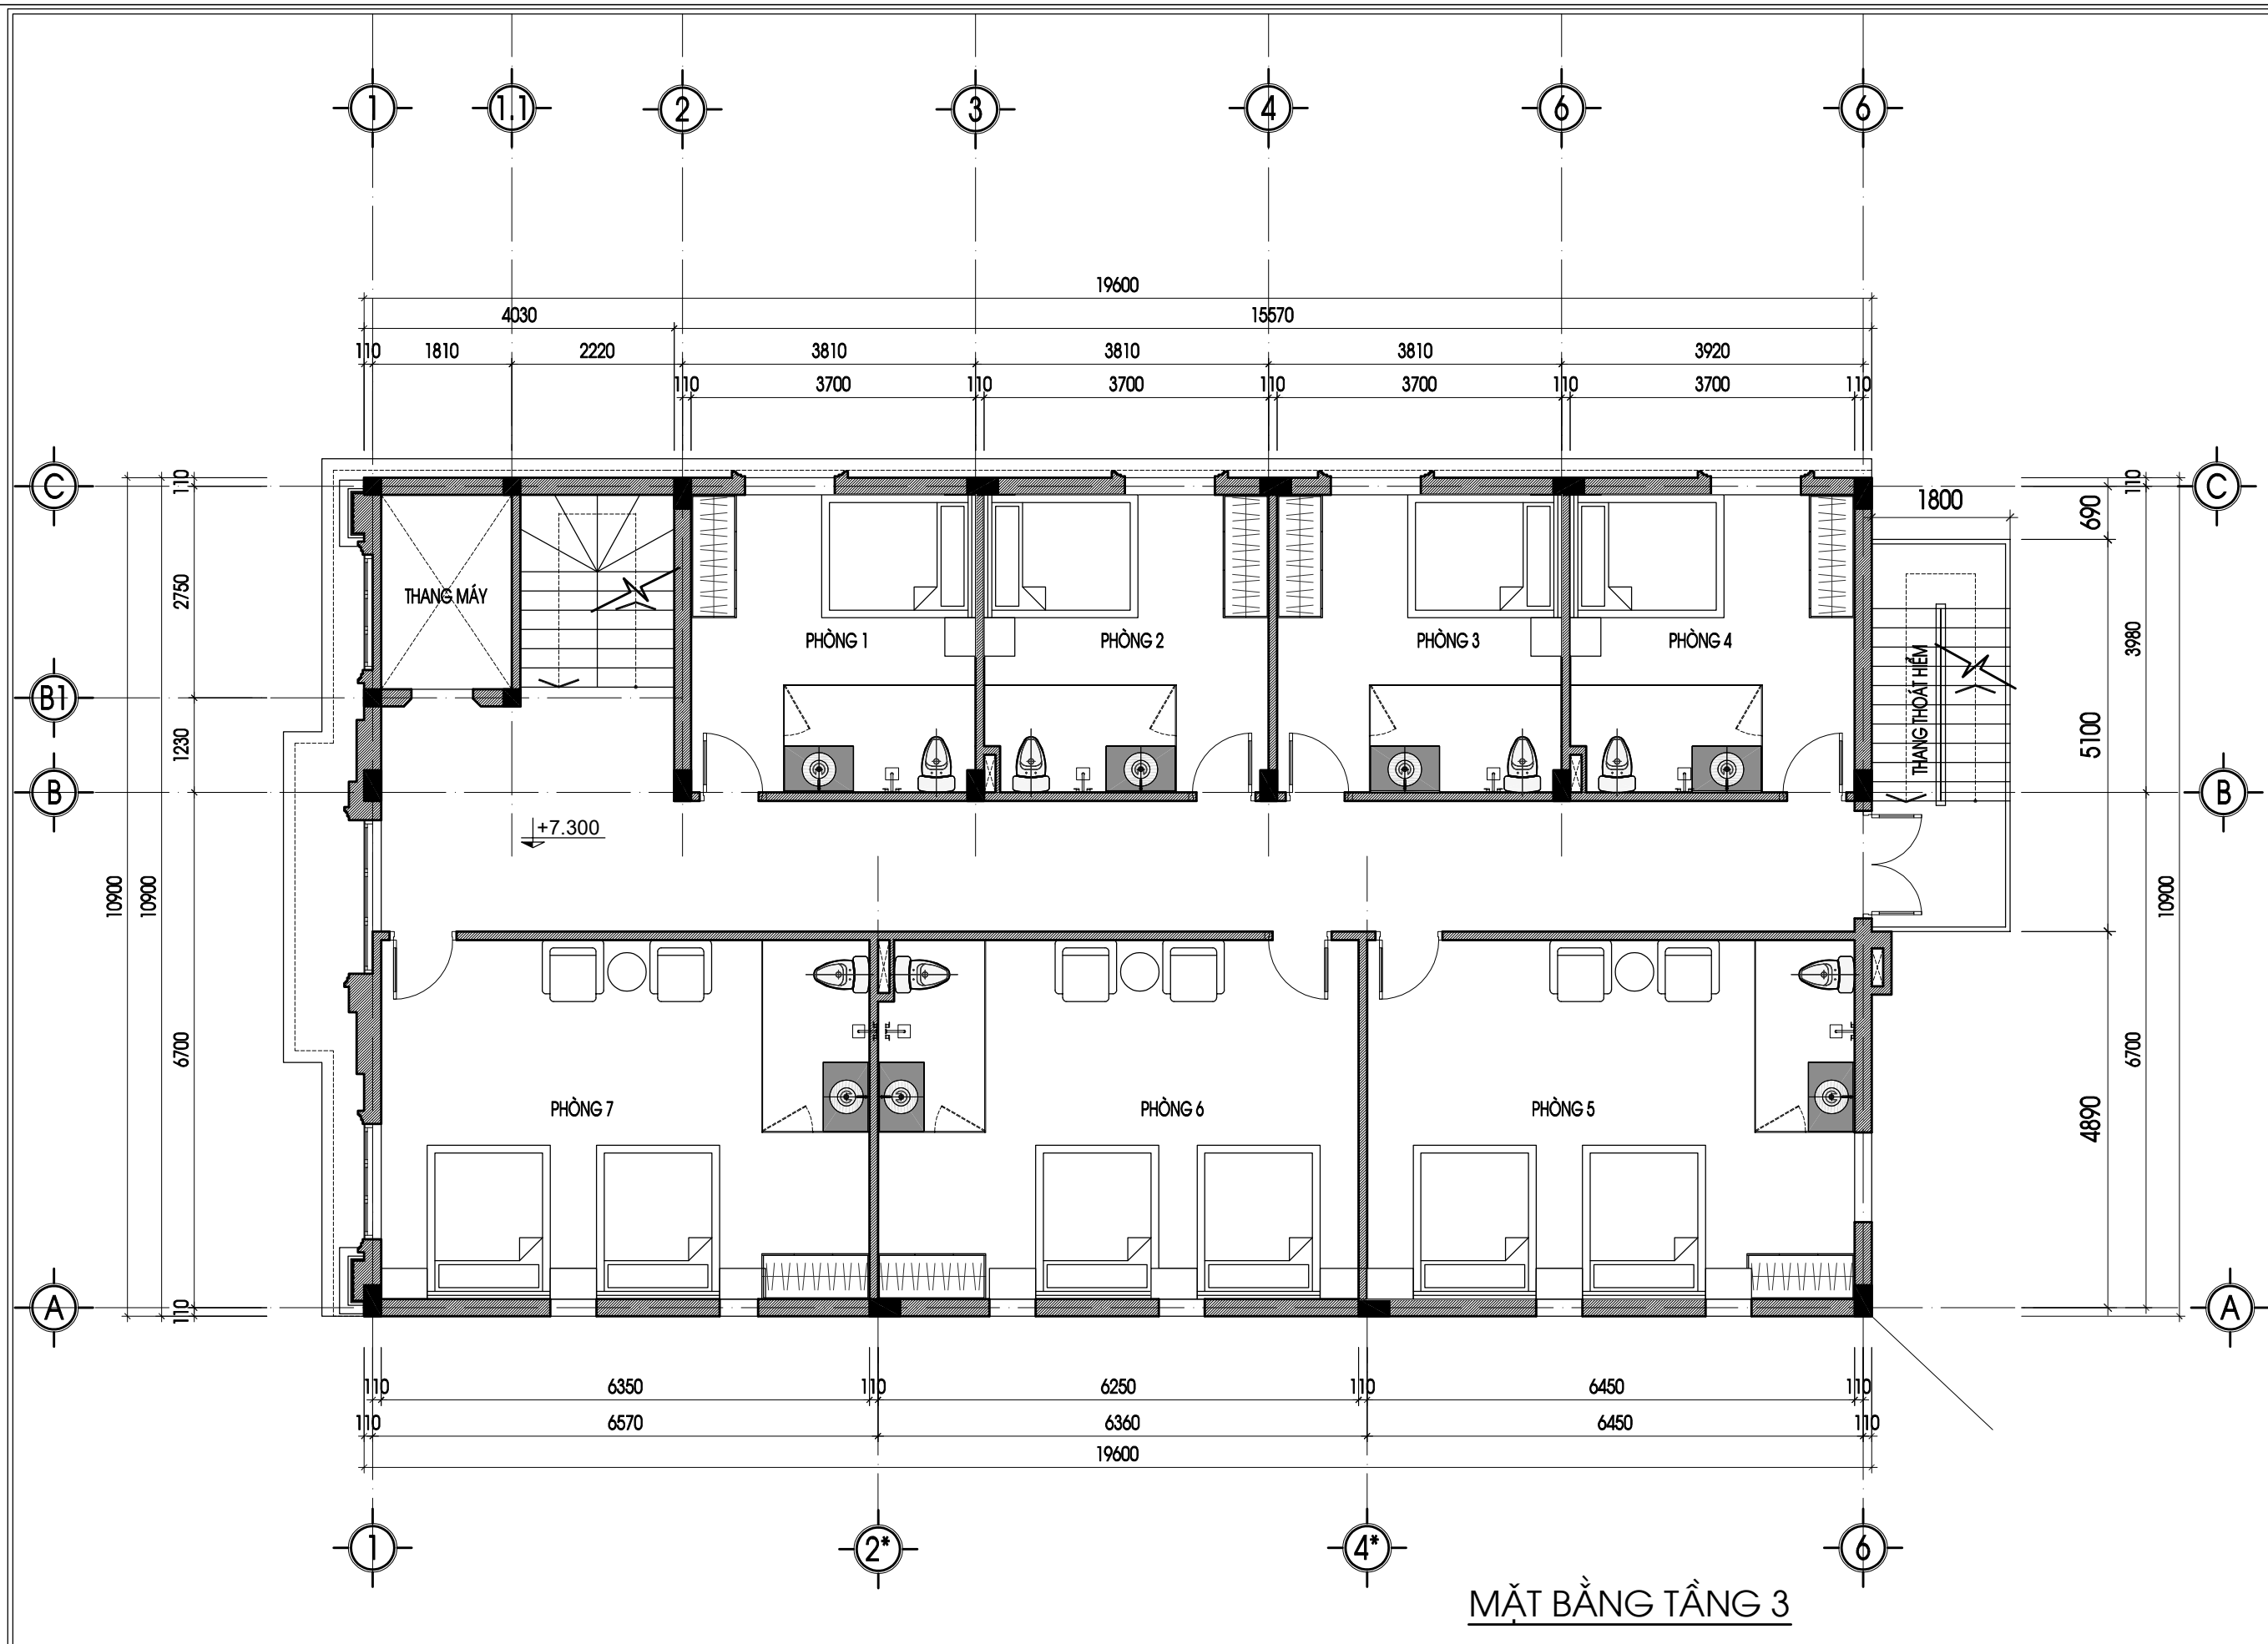

MẶT BẰNG TẦNG 3

CHỦ ĐẦU TƯ

ANH SỸ

CÔNG TRÌNH

KHÁCH SẠN

ĐỊA ĐIỂM

YÊN LỆNH, THÁI THUY, HUNG YÊN

ĐƠN VỊ THIẾT KẾ



CÔNG TY CỔ PHẦN
TƯ VẤN THIẾT KẾ HÀ NỘI

ĐC: SN71 SƠN ĐỒNG, HÀ NỘI
TEL: 0983.381.930

GIÁM ĐỐC

(Signature)

NGUYỄN ĐỨC MINH

CHỦ TRÌ DỰ ÁN

(Signature)

KTS. NGUYỄN ĐỨC MINH

THIẾT KẾ

(Signature)

KTS. NGUYỄN DOÀN HIẾU

KẾT CẤU

(Signature)

KS. TRẦN VĂN ANH

GIẢI ĐOẠN

H.S.X.P

HẠNG MỤC

Kiến trúc

TÊN BẢN VẼ


MẶT BẰNG TẦNG 3

HOÀN THÀNH

02/2026

KÝ HIỆU BẢN VẼ

KT-04

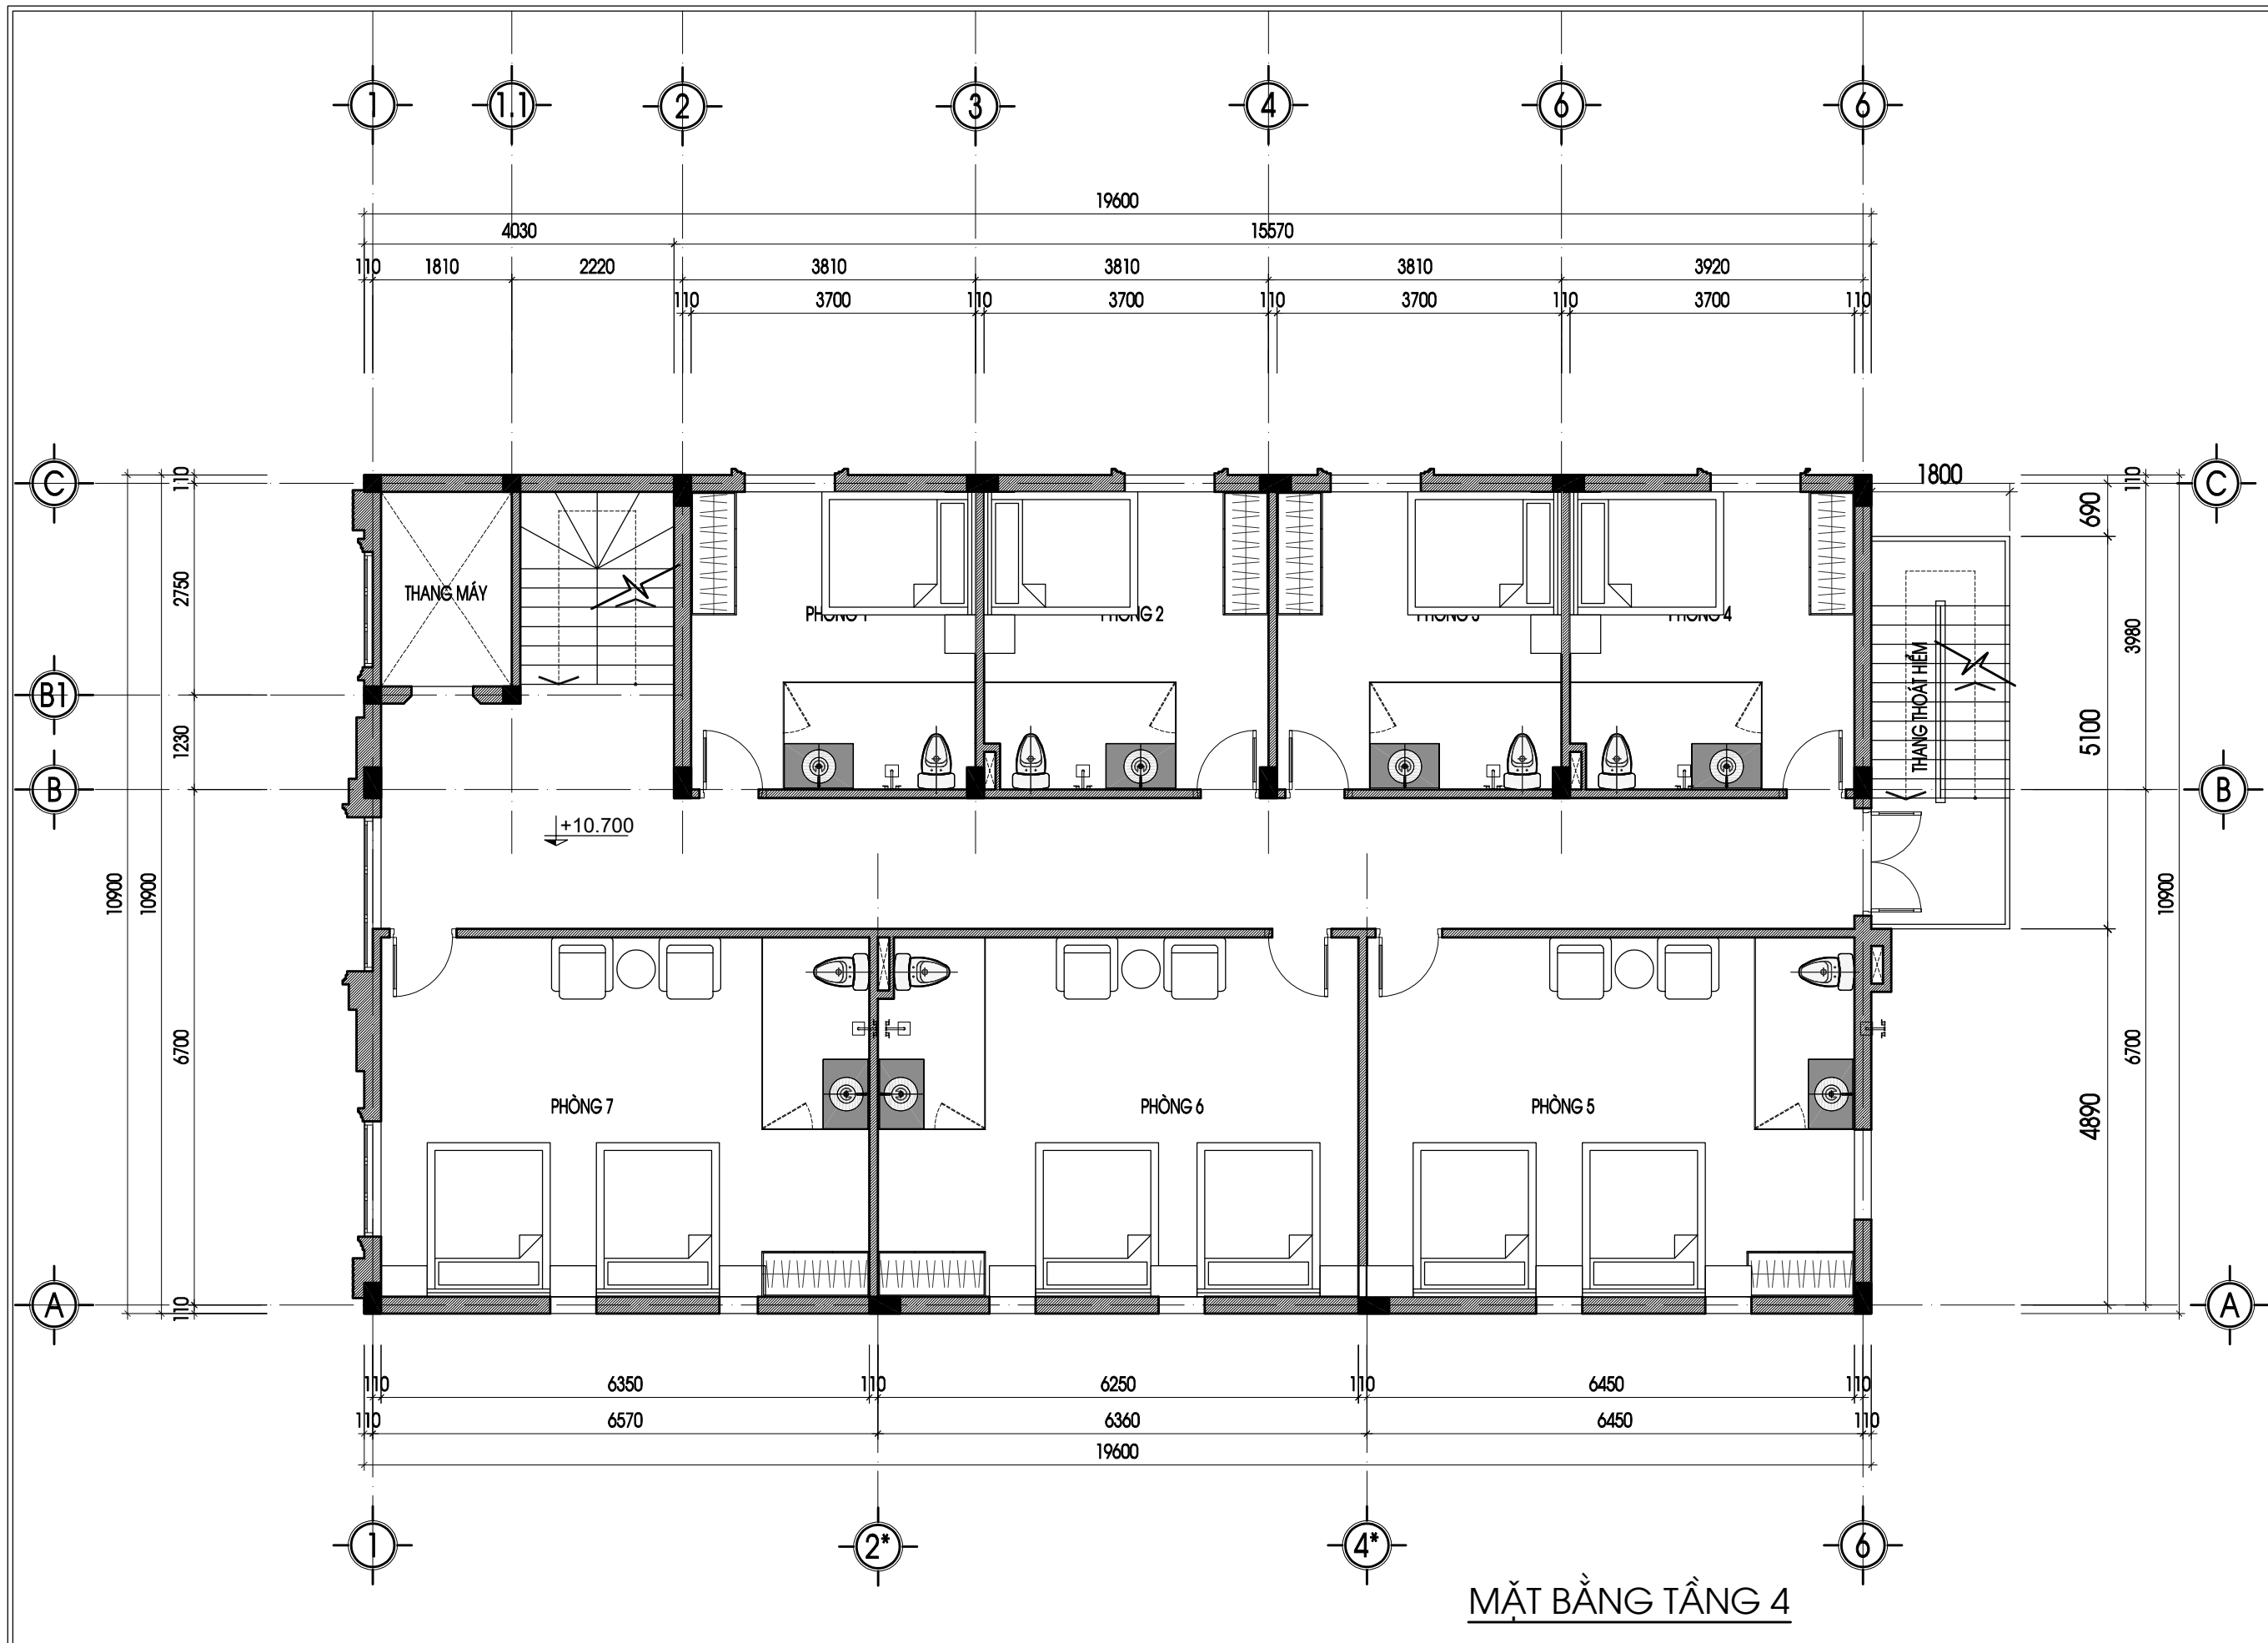

MẶT BẰNG TẦNG 4

CHỦ ĐẦU TƯ

ANH SỸ

CÔNG TRÌNH

KHÁCH SẠN

ĐỊA ĐIỂM

YÊN LỆNH, THÁI THUY, HUNG YÊN

ĐƠN VỊ THIẾT KẾ



CÔNG TY CỔ PHẦN
TƯ VẤN THIẾT KẾ HÀ NỘI

ĐC: SN71 SƠN ĐỒNG, HÀ NỘI
TEL: 0983.381.930

GIÁM ĐỐC

(Signature)

NGUYỄN ĐỨC MINH

CHỦ TRÌ DỰ ÁN

(Signature)

KTS. NGUYỄN ĐỨC MINH

THIẾT KẾ

(Signature)

KTS. NGUYỄN DOÀN HIẾU

KẾT CẤU

(Signature)

KS. TRẦN VĂN ANH

GIẢI ĐOẠN

H.S.X.P

HẠNG MỤC

KIẾN TRÚC

TÊN BẢN VẼ


MẶT BẰNG TẦNG 4

HOÀN THÀNH

02/2026

KÝ HIỆU BẢN VẼ

KT-05

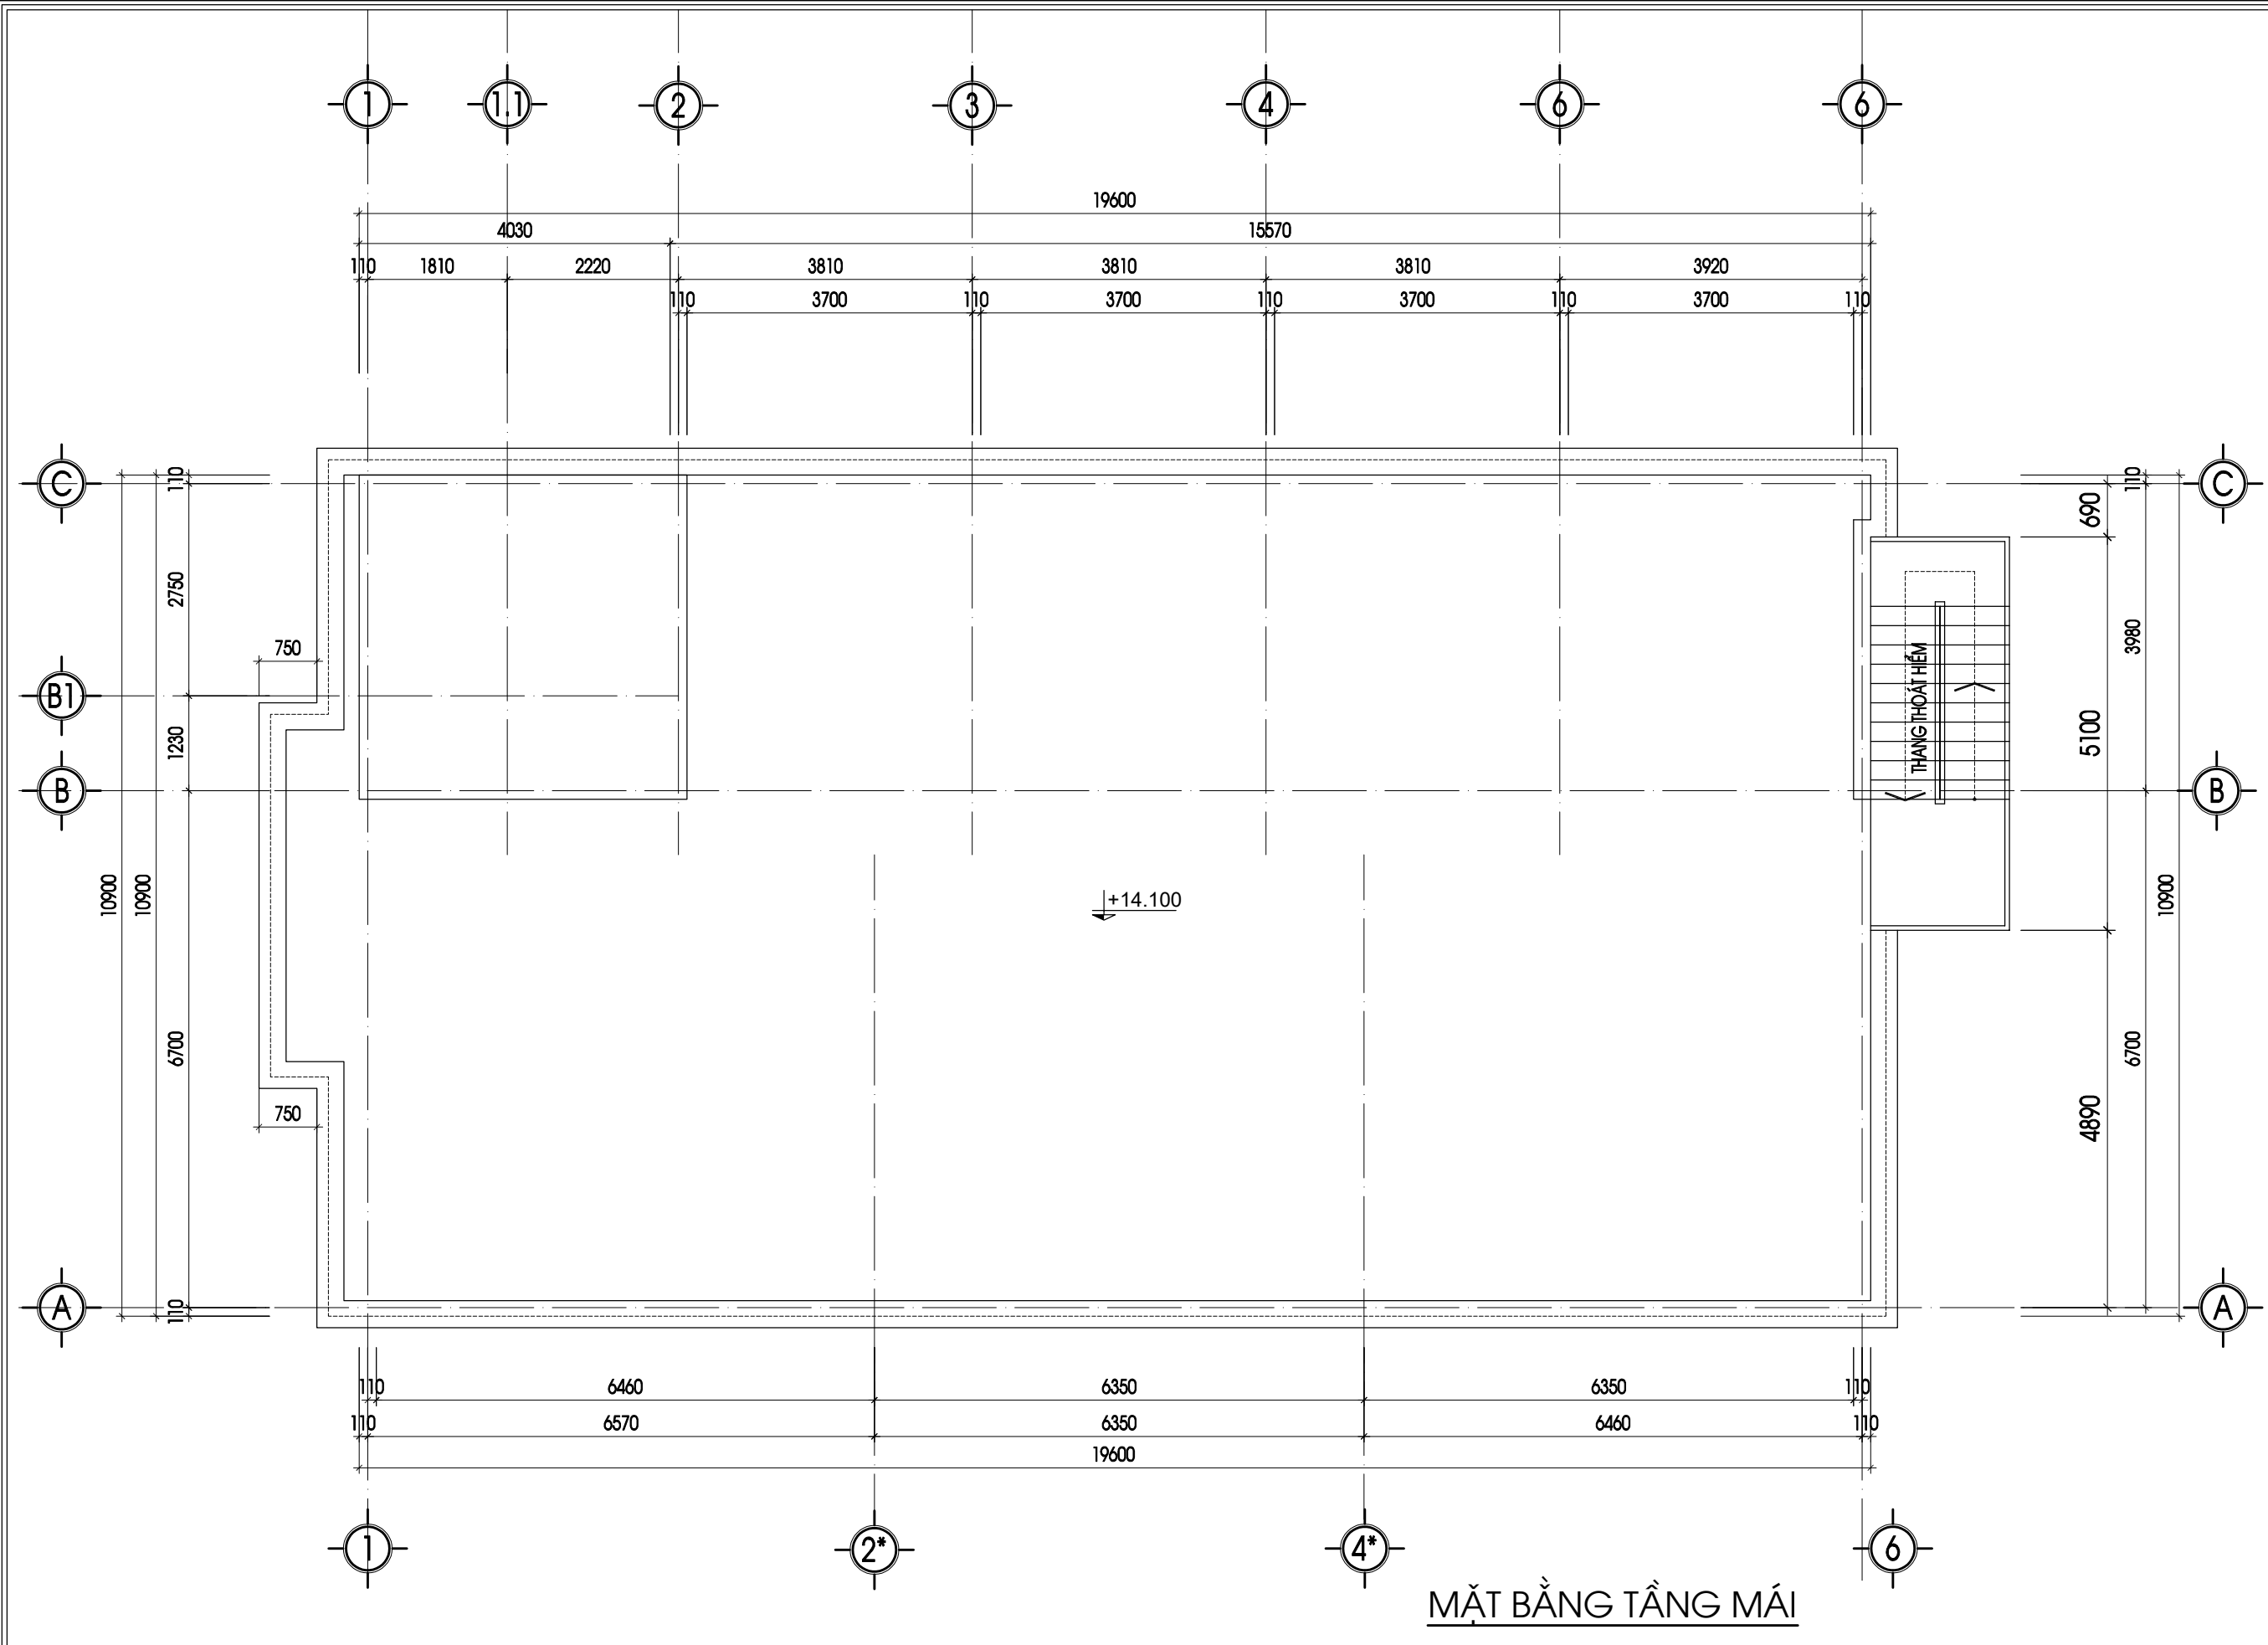

MẶT BẰNG TẦNG MÁI

CHỦ ĐẦU TƯ

ANH SỸ

CÔNG TRÌNH

KHÁCH SẠN

ĐỊA ĐIỂM

YÊN LỆNH, THÁI THUY, HUNG YÊN

ĐƠN VỊ THIẾT KẾ



CÔNG TY CỔ PHẦN
TƯ VẤN THIẾT KẾ HÀ NỘI

ĐC: SN71 SƠN ĐỒNG, HÀ NỘI
TEL: 0983.381.930

GIÁM ĐỐC

(Signature)

NGUYỄN ĐỨC MINH

CHỦ TRÌ DỰ ÁN

(Signature)

KTS. NGUYỄN ĐỨC MINH

THIẾT KẾ

(Signature)

KTS. NGUYỄN DOÀN HIẾU

KẾT CẤU

(Signature)

KS. TRẦN VĂN ANH

GIẢI ĐOẠN

H.S.X.P

HẠNG MỤC

Kiến trúc

TÊN BẢN VẼ


MẶT BẰNG TẦNG MÁI

HOÀN THÀNH

02/2026

KÝ HIỆU BẢN VẼ

KT-06

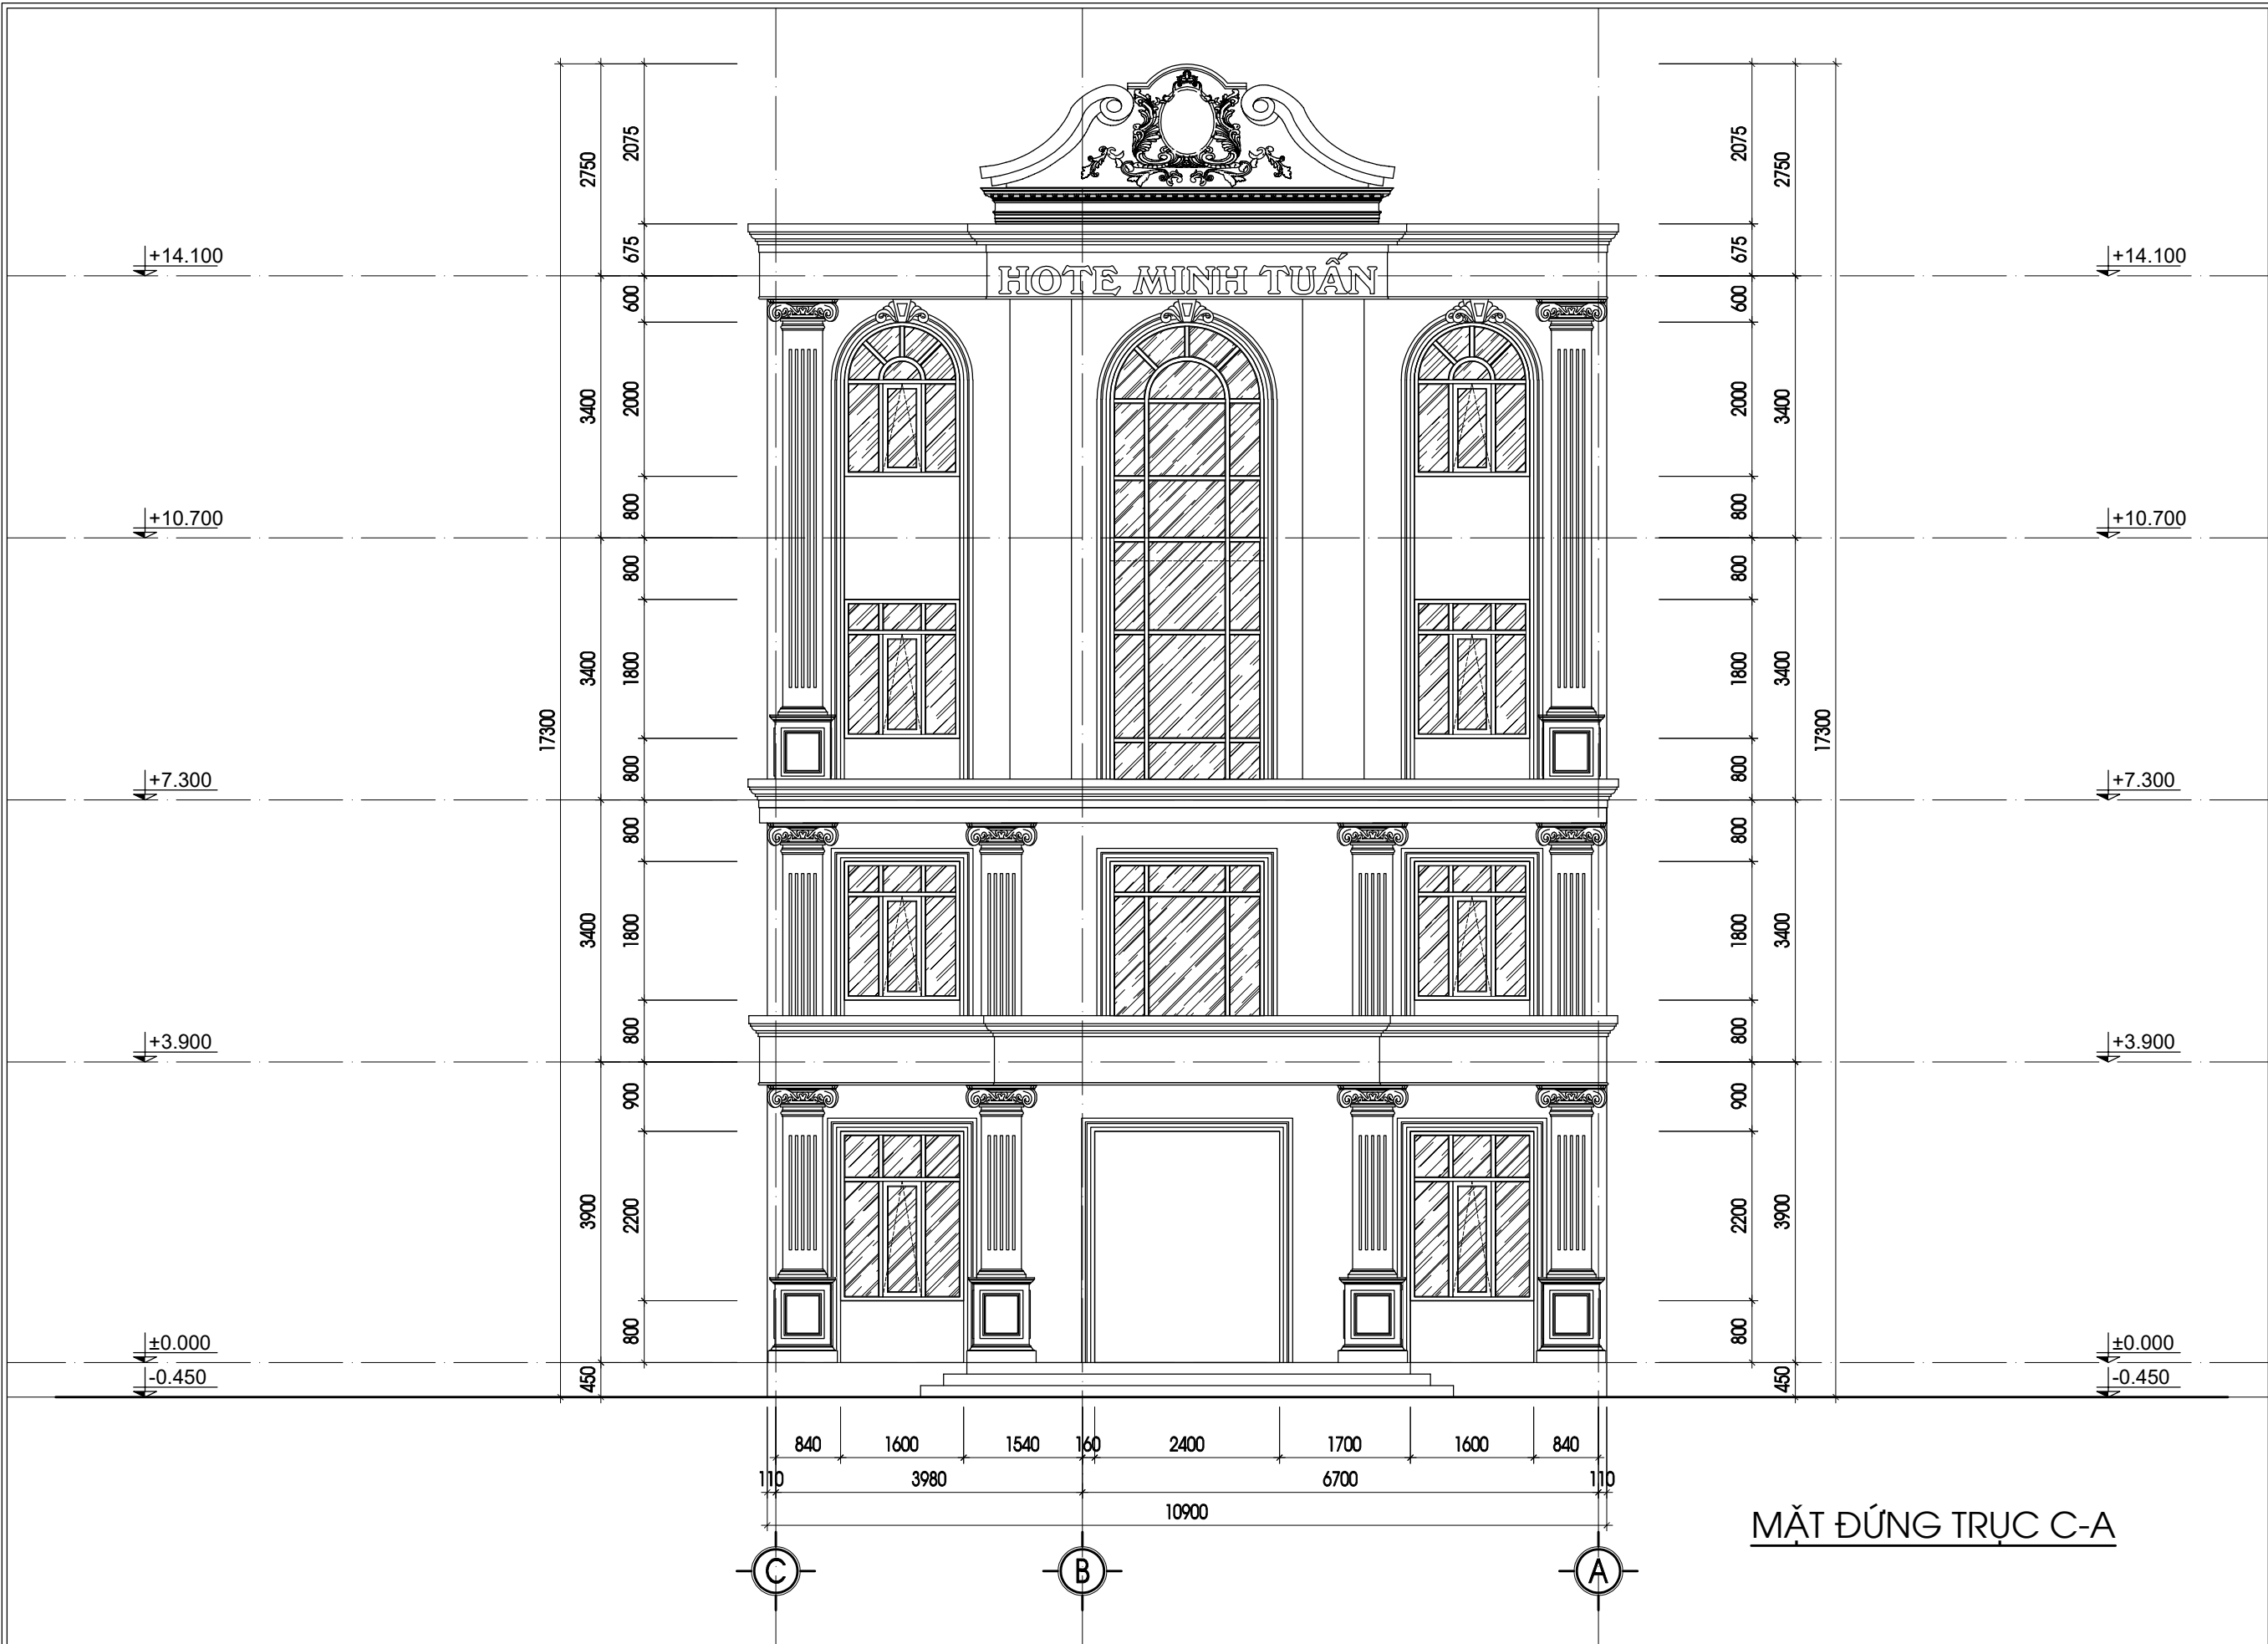

CHỦ ĐẦU TƯ

ANH SỸ

CÔNG TRÌNH

KHÁCH SẠN

ĐỊA ĐIỂM

YÊN LỆNH, THÁI THUY, HUNG YÊN

ĐƠN VỊ THIẾT KẾ



CÔNG TY CỔ PHẦN
TƯ VẤN THIẾT KẾ HÀ NỘI

ĐC: SN71 SƠN ĐỒNG, HÀ NỘI
TEL: 0983.381.930

GIÁM ĐỐC

(Signature)

NGUYỄN ĐỨC MINH

CHỦ TRÌ DỰ ÁN

(Signature)

KTS. NGUYỄN ĐỨC MINH

THIẾT KẾ

(Signature)

KTS. NGUYỄN DOÀN HIẾU

KẾT CẤU

(Signature)

KS. TRẦN VĂN ANH

GIẢI ĐOẠN

H.S.X.P

HẠNG MỤC

KIẾN TRÚC

TÊN BẢN VẼ

MẶT ĐỨNG TRỤC C-A


HOÀN THÀNH

02/2026

KÝ HIỆU BẢN VẼ

KT-07

MẶT ĐỨNG TRỤC C-A

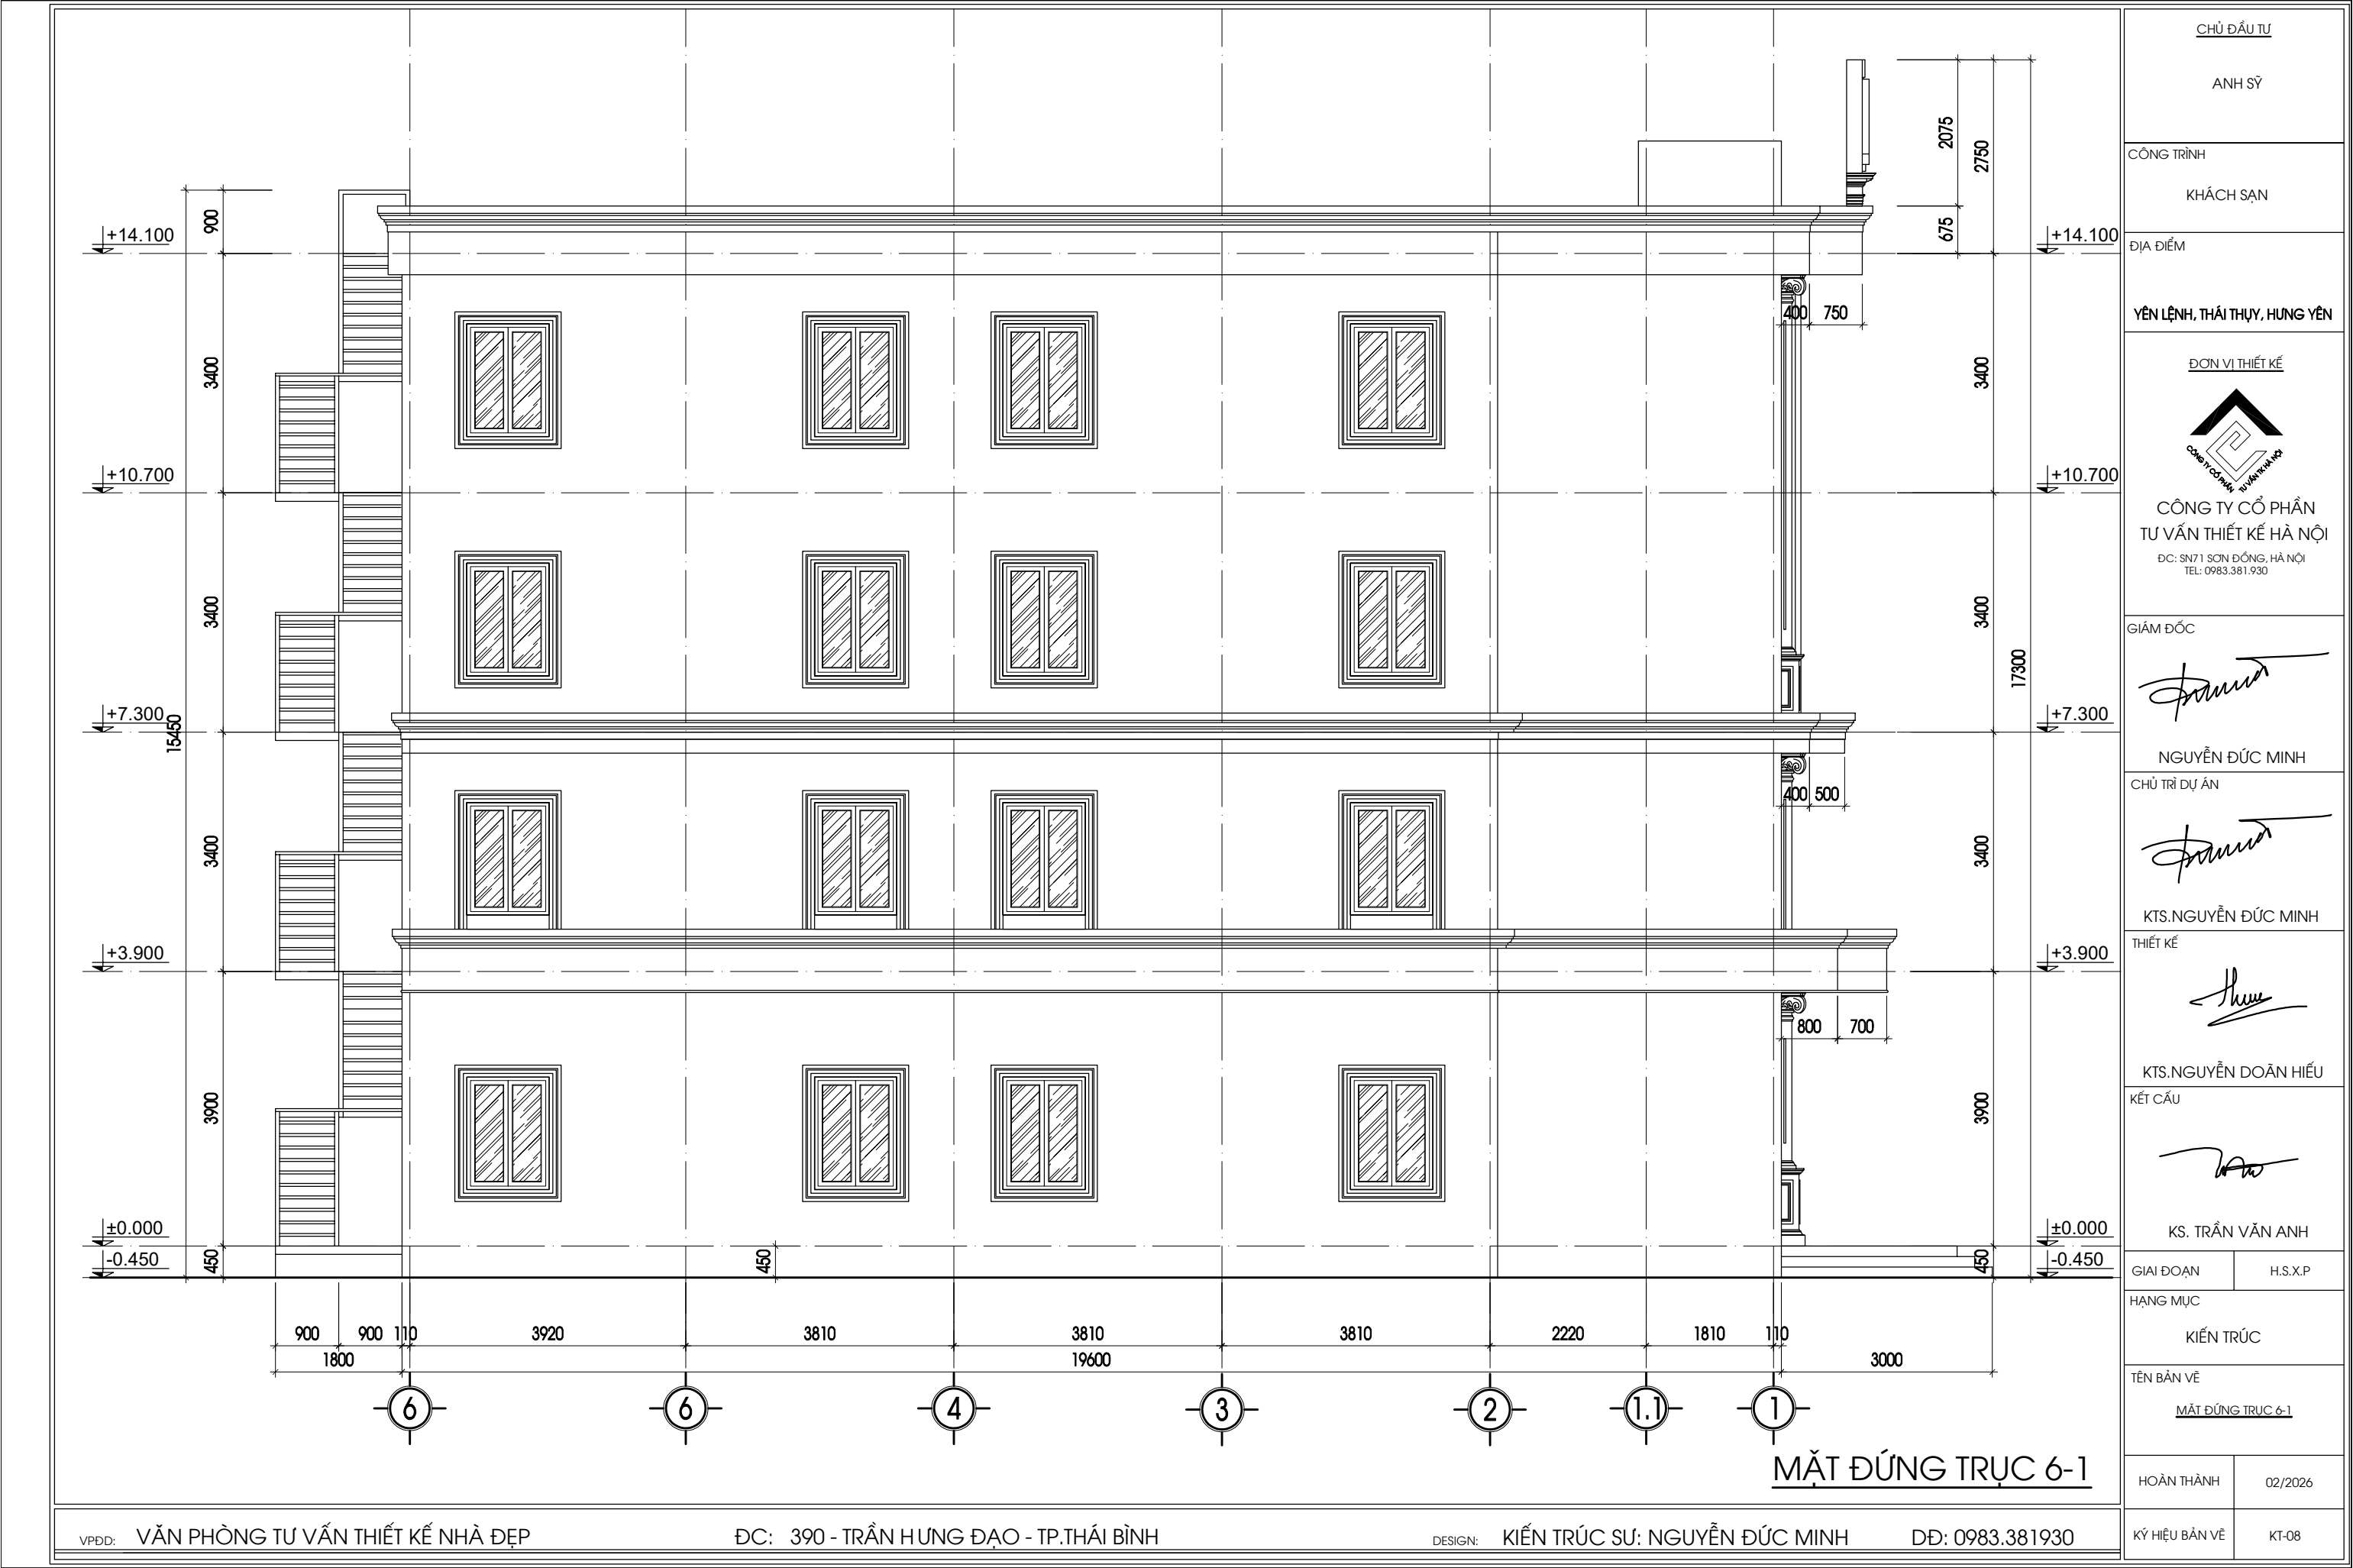

CHỦ ĐẦU TƯ

ANH SỸ

CÔNG TRÌNH

KHÁCH SẠN

ĐỊA ĐIỂM

YÊN LỆNH, THÁI THUY, HUNG YÊN

ĐƠN VỊ THIẾT KẾ



CÔNG TY CỔ PHẦN
TƯ VẤN THIẾT KẾ HÀ NỘI

ĐC: SN71 SƠN ĐỒNG, HÀ NỘI
TEL: 0983.381.930

GIÁM ĐỐC

Nguyễn Đức Minh

NGUYỄN ĐỨC MINH

CHỦ TRÌ DỰ ÁN

Nguyễn Đức Minh

KTS. NGUYỄN ĐỨC MINH

THIẾT KẾ

Nguyễn Đoàn Hiếu

KTS. NGUYỄN ĐOÀN HIẾU

KẾT CẤU

Trần Văn Anh

KS. TRẦN VĂN ANH

GIAI ĐOẠN

H.S.X.P

HẠNG MỤC

KIẾN TRÚC

TÊN BẢN VẼ

MẶT ĐÚNG TRỤC 6-1

HOÀN THÀNH

02/2026

KÝ HIỆU BẢN VẼ

KT-08


VPDD: VĂN PHÒNG TƯ VẤN THIẾT KẾ NHÀ ĐẸP

ĐC: 390 - TRẦN HUNG ĐẠO - TP.THÁI BÌNH

DESIGN: KIẾN TRÚC SƯ: NGUYỄN ĐỨC MINH

ĐD: 0983.381930

MẶT ĐÚNG TRỤC 6-1

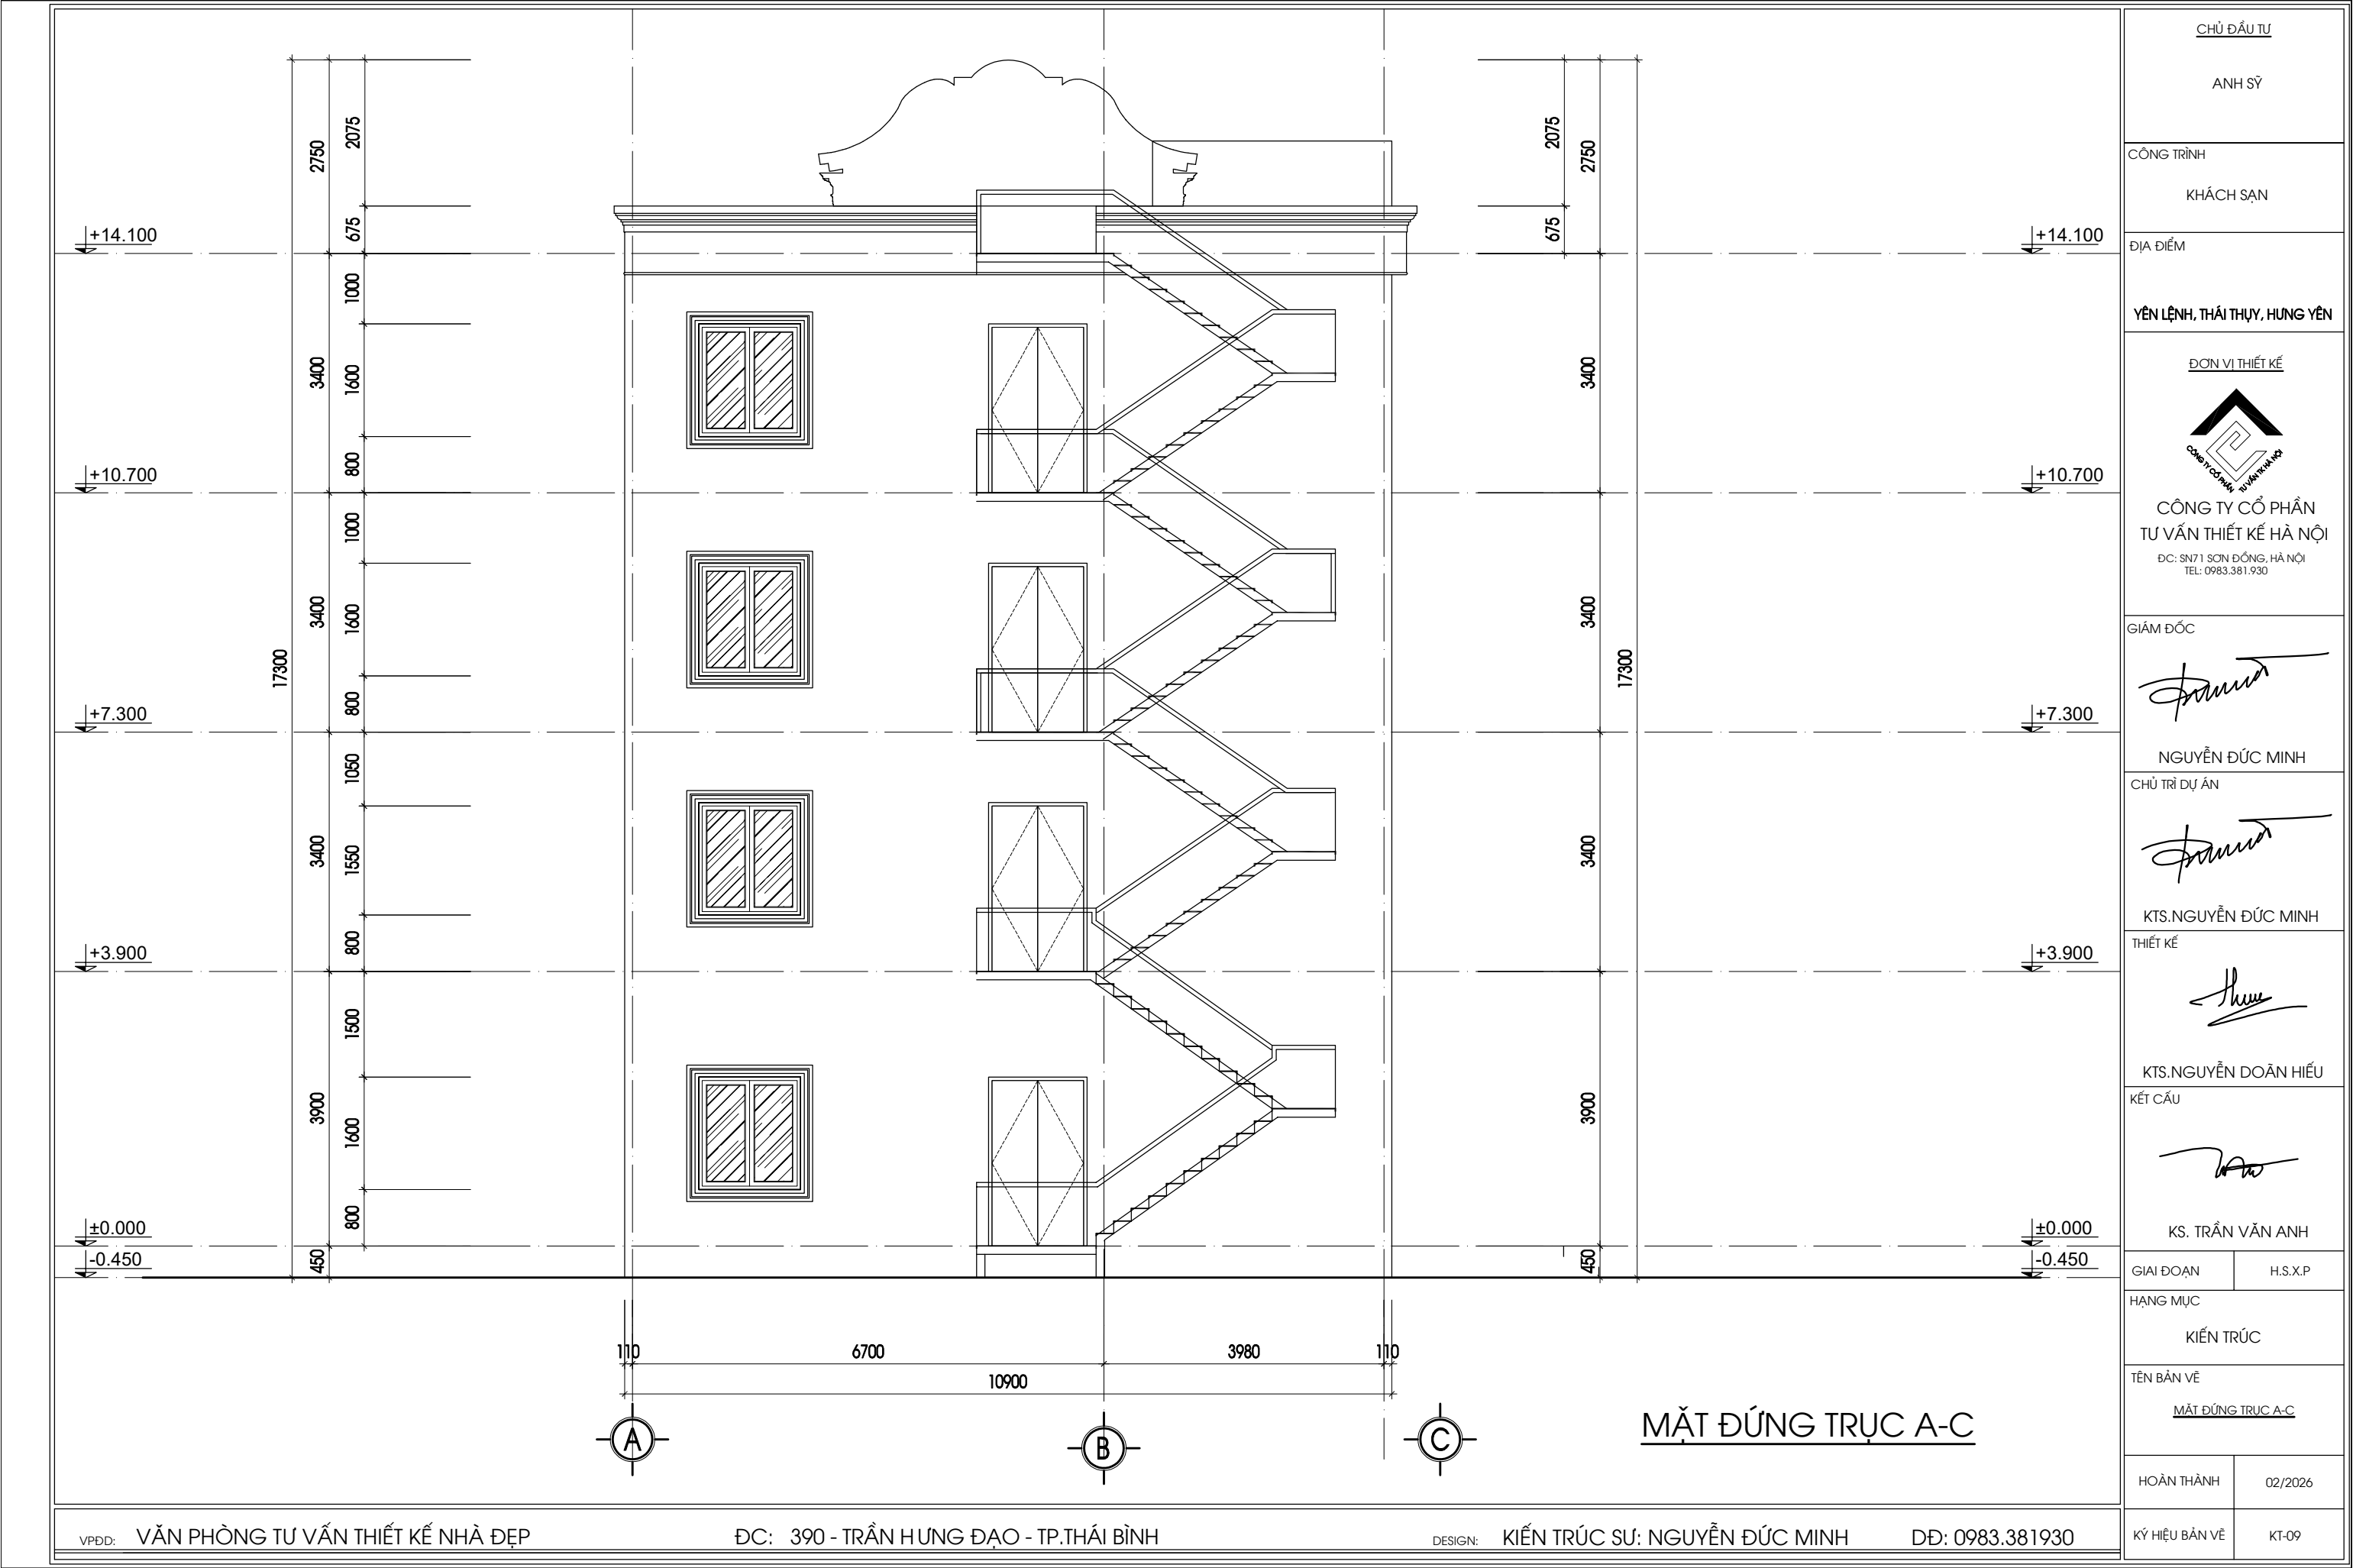

CHỦ ĐẦU TƯ

ANH SỸ

CÔNG TRÌNH

KHÁCH SẠN

ĐỊA ĐIỂM

YÊN LỆNH, THÁI THUY, HUNG YÊN

ĐƠN VỊ THIẾT KẾ



CÔNG TY CỔ PHẦN
TƯ VẤN THIẾT KẾ HÀ NỘI

ĐC: SN71 SƠN ĐỒNG, HÀ NỘI
TEL: 0983.381.930

GIÁM ĐỐC

(Signature)

NGUYỄN ĐỨC MINH

CHỦ TRÌ DỰ ÁN

(Signature)

KTS. NGUYỄN ĐỨC MINH

THIẾT KẾ

(Signature)

KTS. NGUYỄN DOÀN HIẾU

KẾT CẤU

(Signature)

KS. TRẦN VĂN ANH

GIẢI ĐOẠN

H.S.X.P

HẠNG MỤC

Kiến trúc

TÊN BẢN VẼ


MẶT ĐÚNG TRỤC A-C

HOÀN THÀNH

02/2026


KÝ HIỆU BẢN VẼ

KT-09

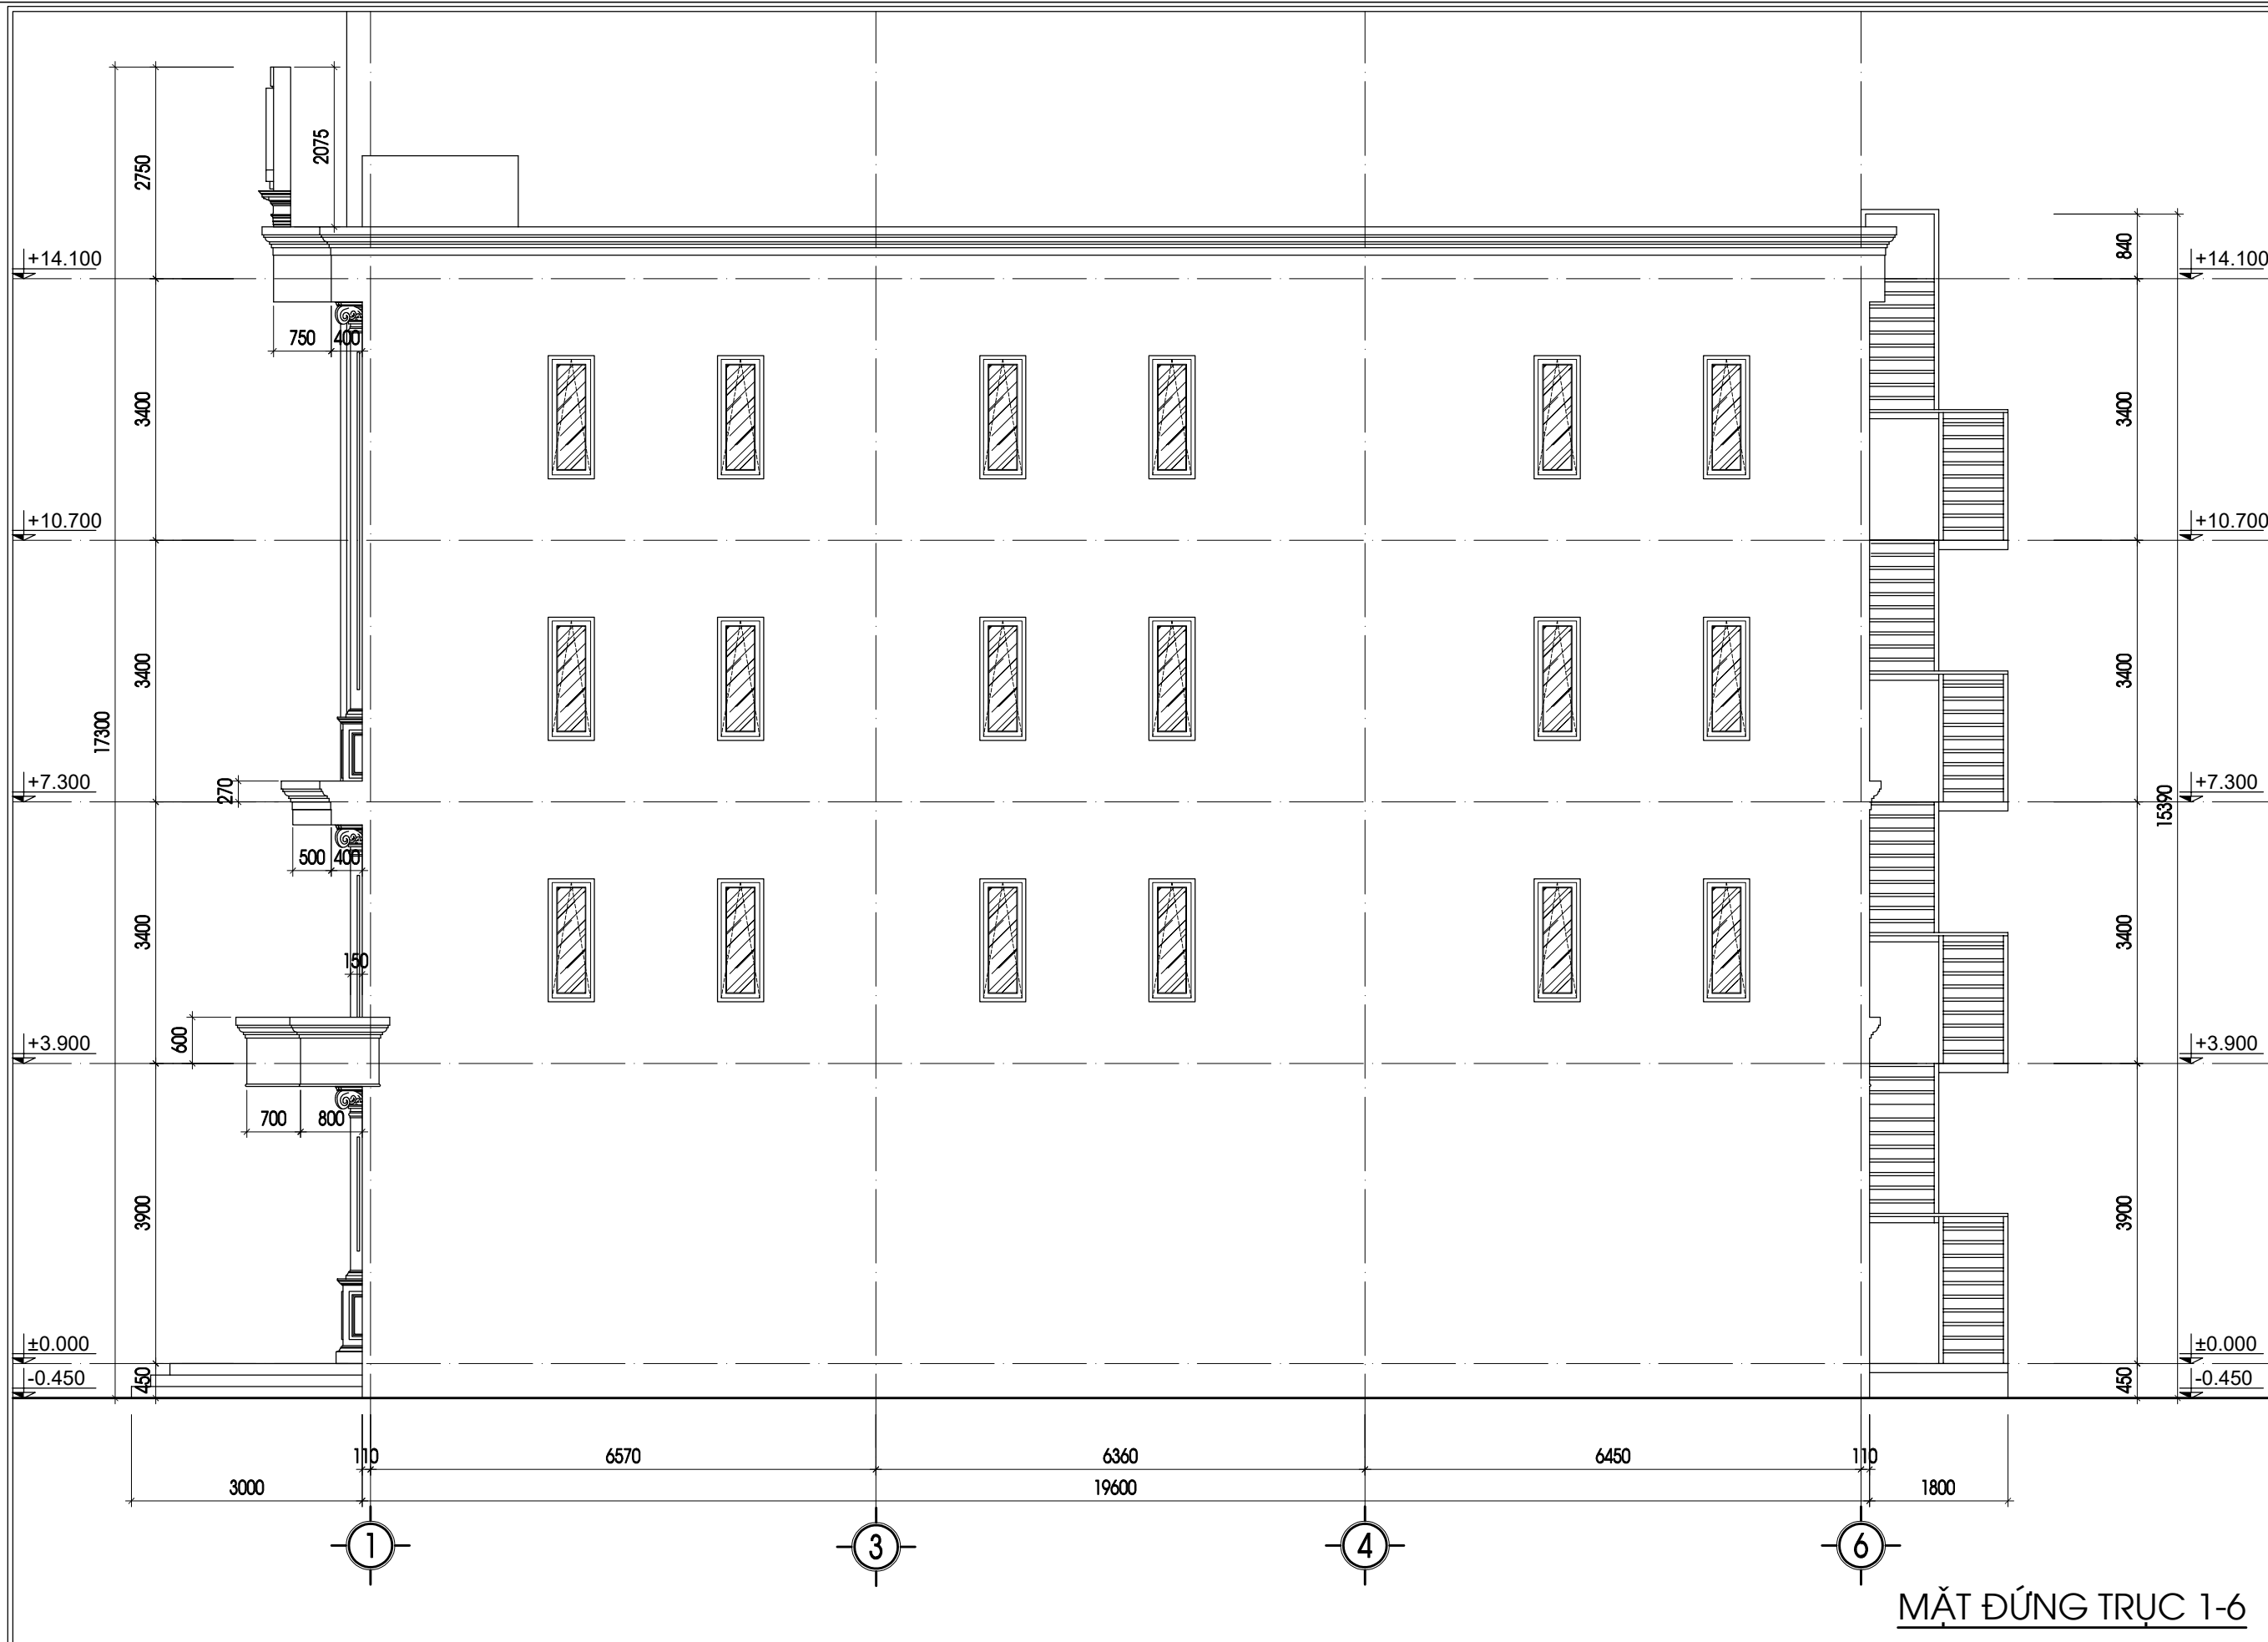

MẶT ĐỨNG TRỤC 1-6

CHỦ ĐẦU TƯ	
ANH SỸ	
CÔNG TRÌNH	
KHÁCH SẠN	
ĐỊA ĐIỂM	
YÊN LỆNH, THÁI THUY, HUNG YÊN	
ĐƠN VỊ THIẾT KẾ	
 CÔNG TY CỔ PHẦN TƯ VẤN THIẾT KẾ HÀ NỘI ĐC: SN71 SƠN ĐỒNG, HÀ NỘI TEL: 0983.381.930	
GIÁM ĐỐC	
 NGUYỄN ĐỨC MINH	
CHỦ TRÌ DỰ ÁN	
 KTS. NGUYỄN ĐỨC MINH	
THIẾT KẾ	
 KTS. NGUYỄN ĐOÀN HIẾU	
KẾT CẤU	
 KS. TRẦN VĂN ANH	
GIẢI ĐOẠN	H.S.X.P
HẠNG MỤC	
KIẾN TRÚC	
TÊN BẢN VẼ	
MẶT ĐỨNG TRỤC 1-6	
HOÀN THÀNH	02/2026
KÝ HIỆU BẢN VẼ	KT-10

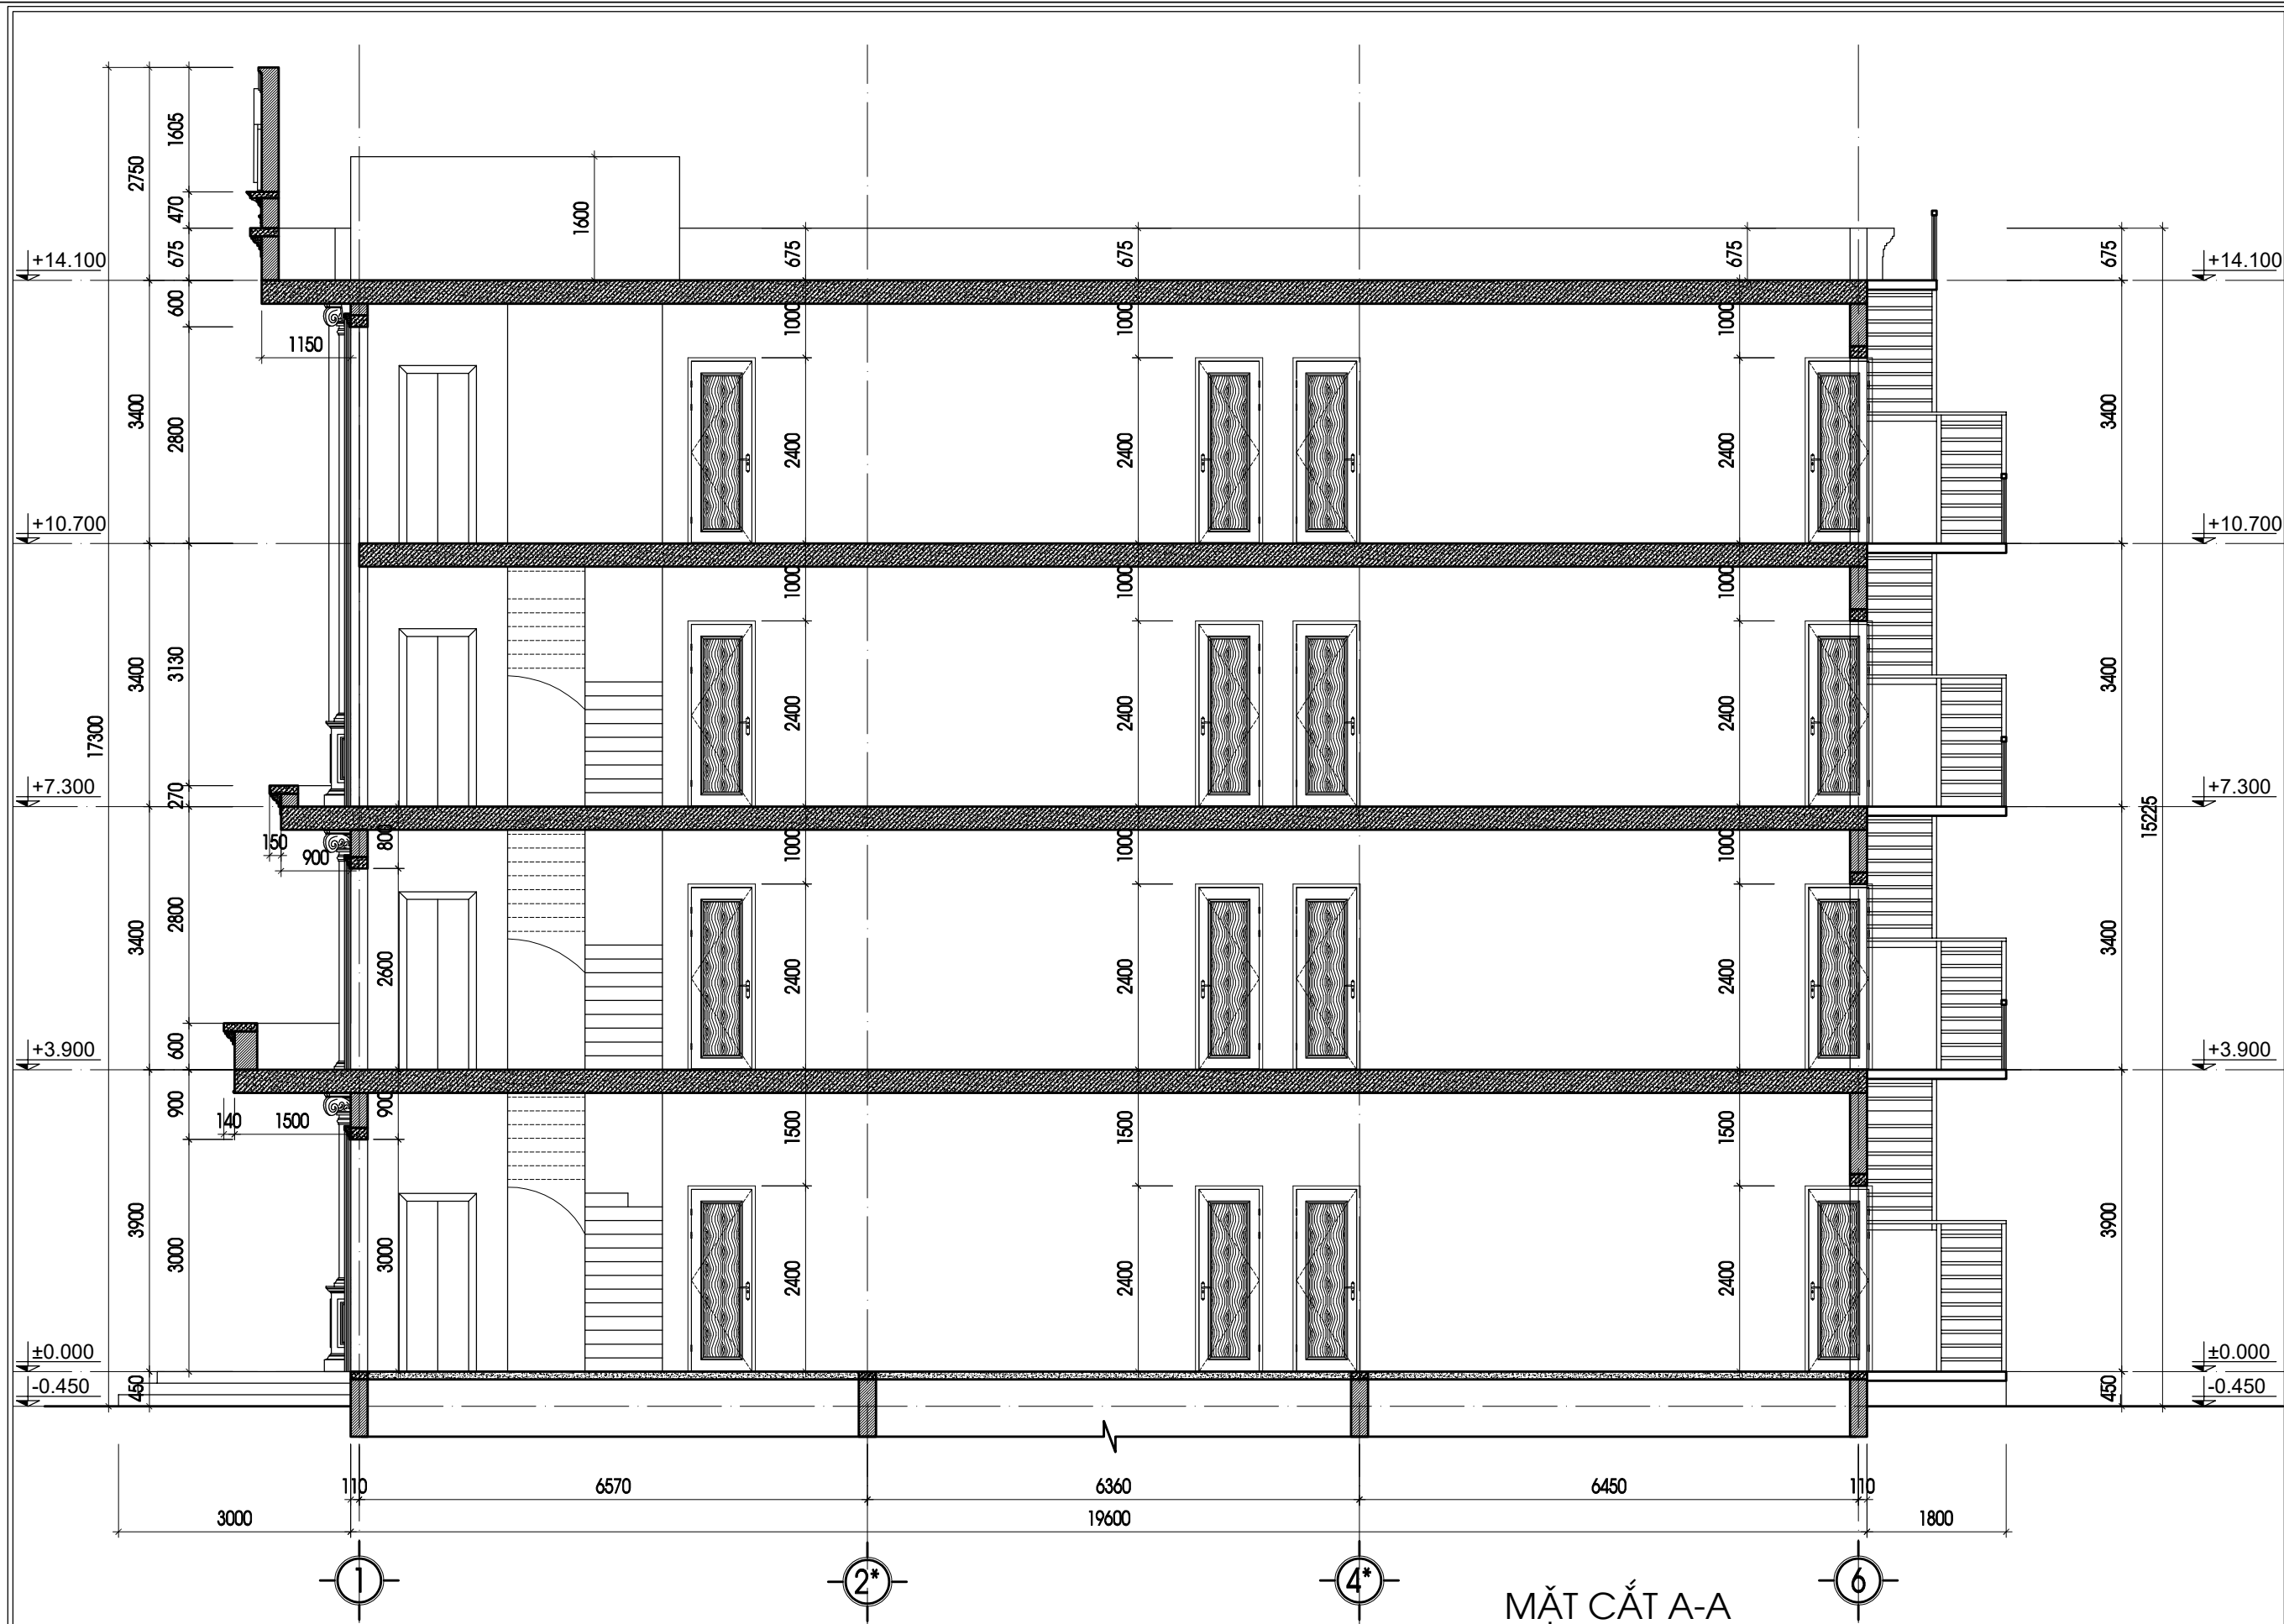

MẶT CẮT A-A

CHỦ ĐẦU TƯ

ANH SỸ

CÔNG TRÌNH

KHÁCH SẠN

ĐỊA ĐIỂM

YÊN LỆNH, THÁI THUY, HUNG YÊN

ĐƠN VỊ THIẾT KẾ



CÔNG TY CỔ PHẦN
TƯ VẤN THIẾT KẾ HÀ NỘI

ĐC: SN71 SƠN ĐỒNG, HÀ NỘI
TEL: 0983.381.930

GIÁM ĐỐC

(Signature)

NGUYỄN ĐỨC MINH

CHỦ TRÌ DỰ ÁN

(Signature)

KTS. NGUYỄN ĐỨC MINH

THIẾT KẾ

(Signature)

KTS. NGUYỄN DOÀN HIẾU

KẾT CẤU

(Signature)

KS. TRẦN VĂN ANH

GIAI ĐOẠN

H.S.X.P

HẠNG MỤC

KIẾN TRÚC

TÊN BẢN VẼ


MẶT CẮT A-A

HOÀN THÀNH

02/2026

KÝ HIỆU BẢN VẼ

KT-11

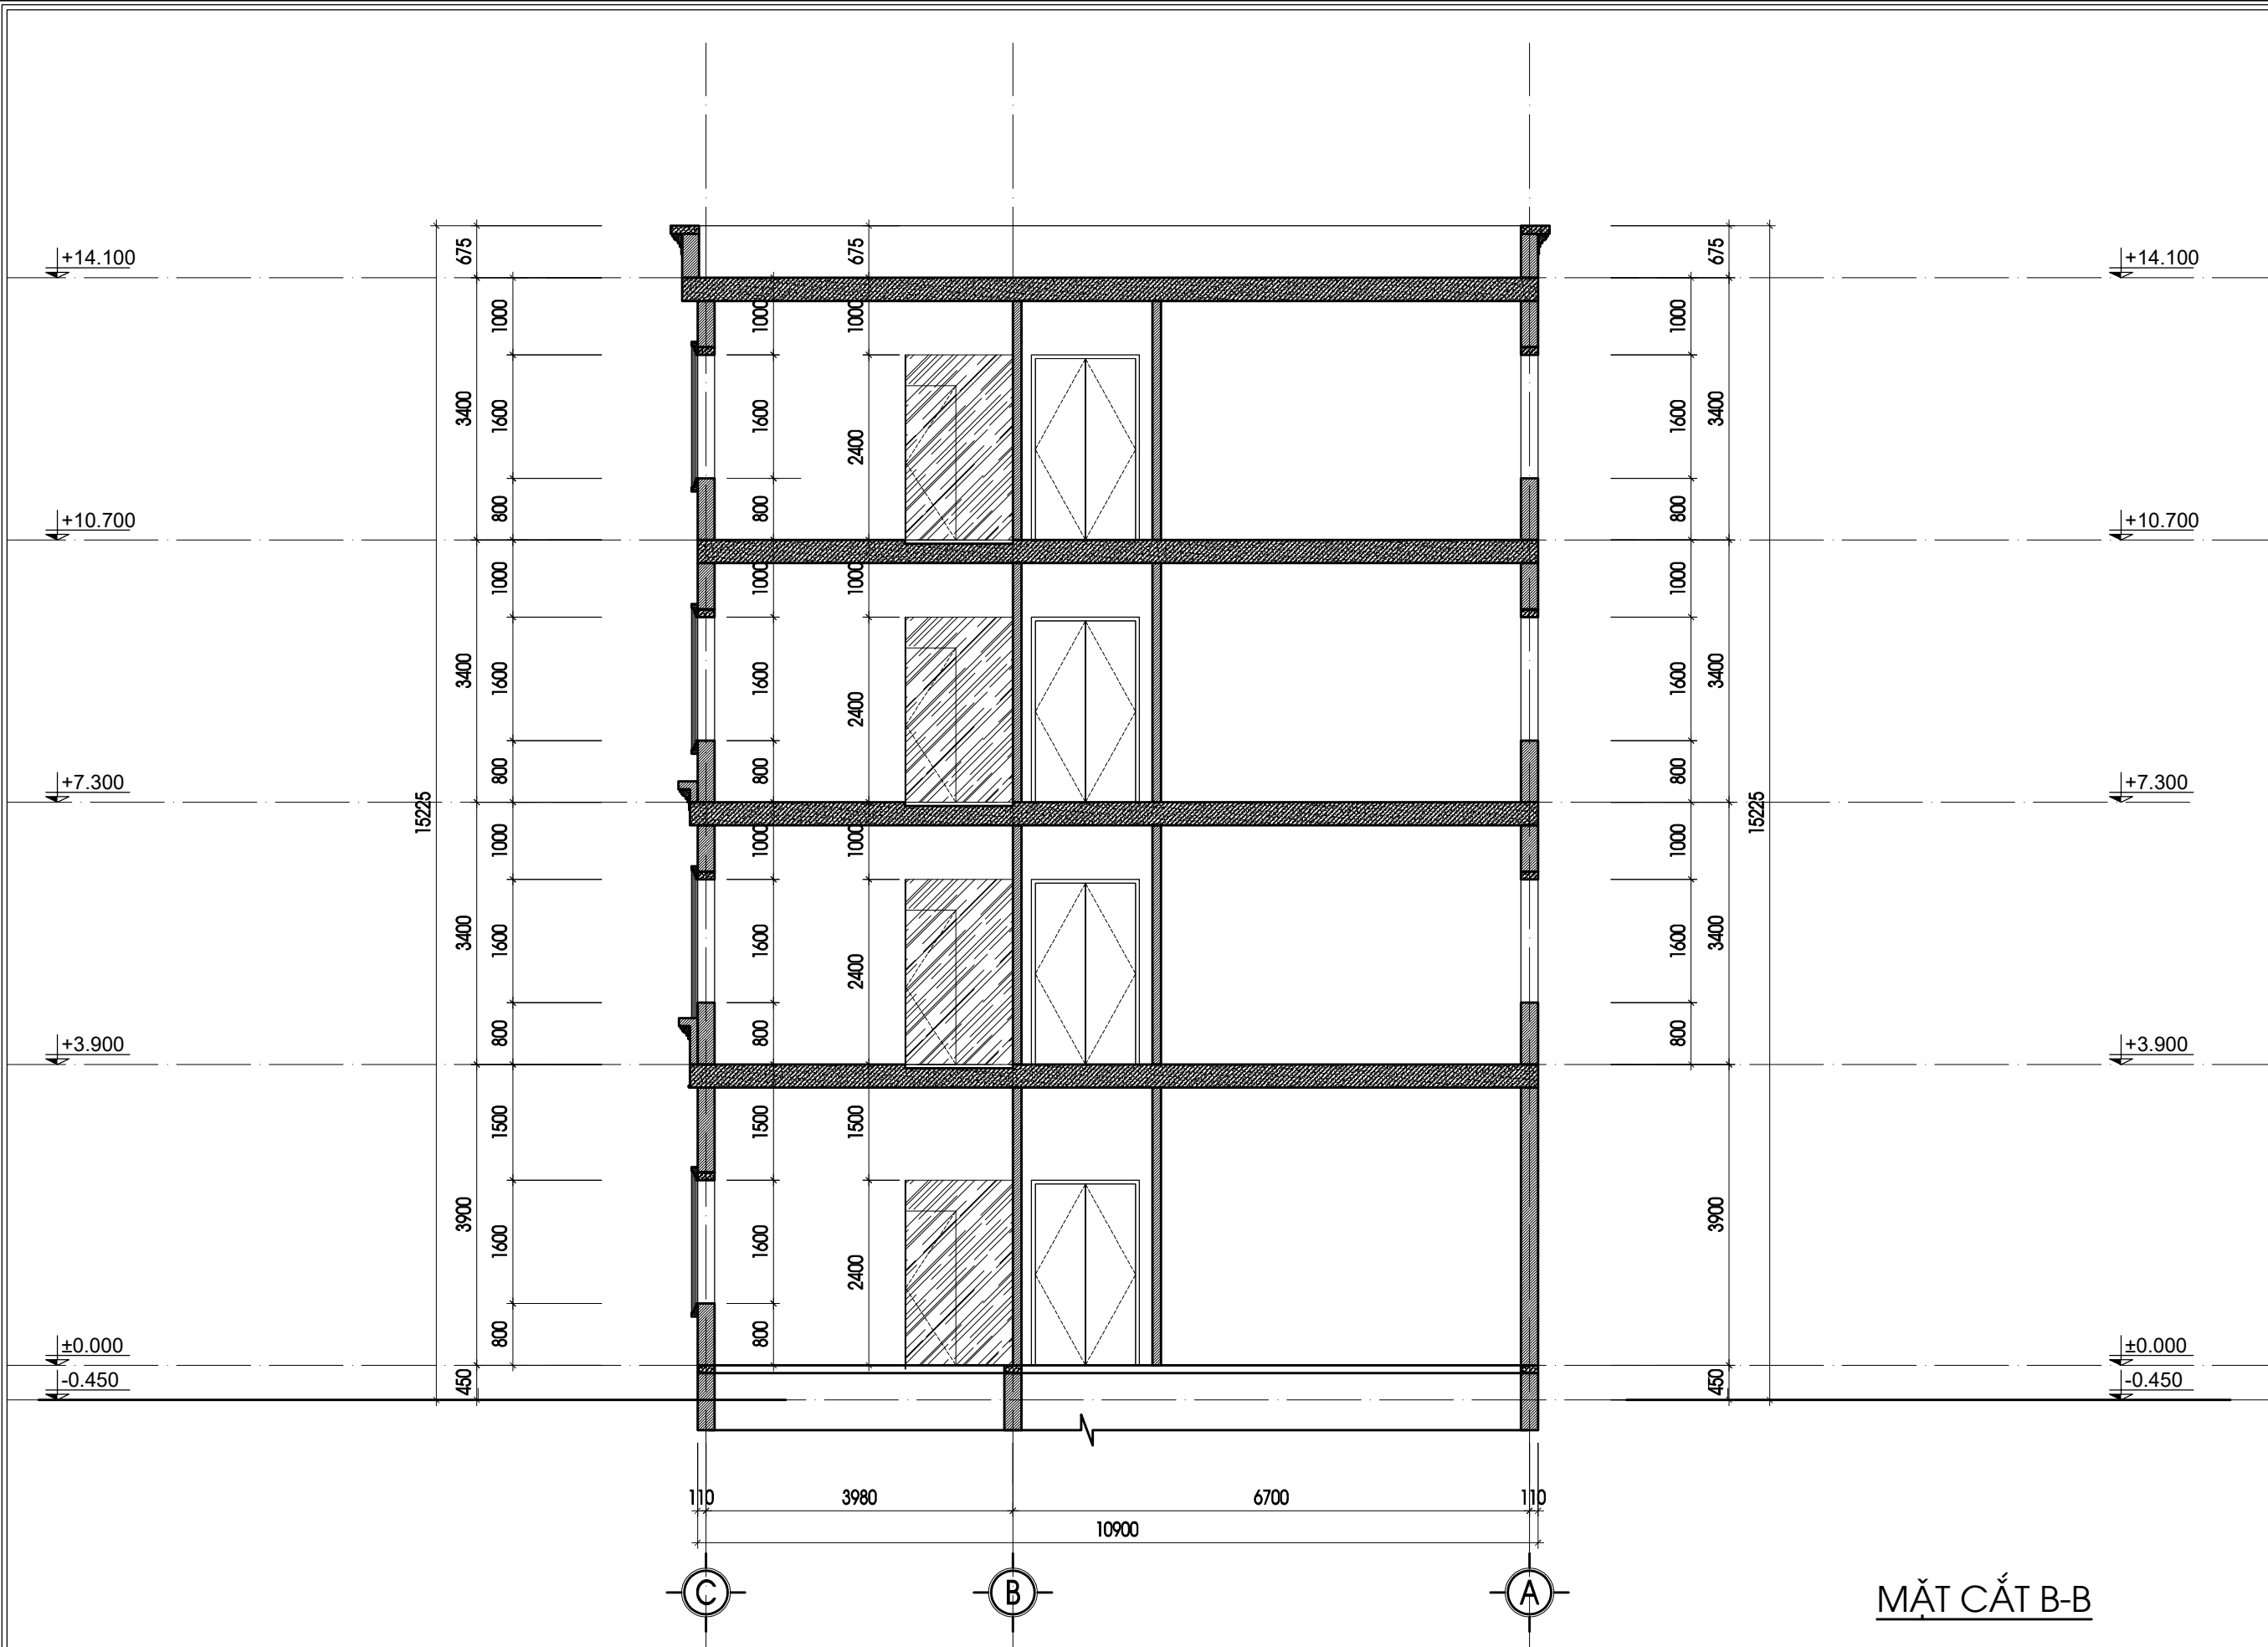

MẶT CẮT B-B

CHỦ ĐẦU TƯ

ANH SỸ

CÔNG TRÌNH

KHÁCH SẠN

ĐỊA ĐIỂM

YÊN LỆNH, THÁI THUY, HUNG YÊN

ĐƠN VỊ THIẾT KẾ



CÔNG TY CỔ PHẦN
TƯ VẤN THIẾT KẾ HÀ NỘI

ĐC: SN71 SƠN ĐỒNG, HÀ NỘI
TEL: 0983.381.930

GIÁM ĐỐC

[Signature]

NGUYỄN ĐỨC MINH

CHỦ TRÌ DỰ ÁN

[Signature]

KTS. NGUYỄN ĐỨC MINH

THIẾT KẾ

[Signature]

KTS. NGUYỄN DOÀN HIẾU

KẾT CẤU

[Signature]

KS. TRẦN VĂN ANH

GIẢI ĐOẠN

H.S.X.P

HẠNG MỤC

KIẾN TRÚC

TÊN BẢN VẼ


MẶT CẮT B-B

HOÀN THÀNH


02/2026

KÝ HIỆU BẢN VẼ


KT-12

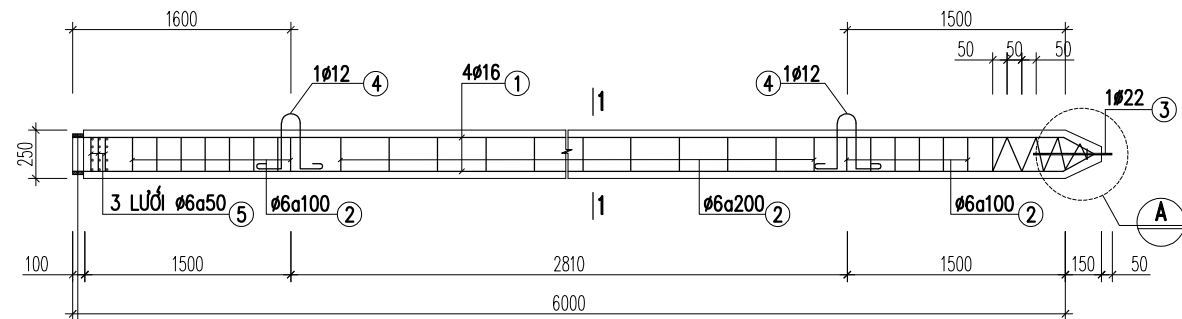


ĐOẠN CỌC MŨI C2 (1 ĐOẠN)

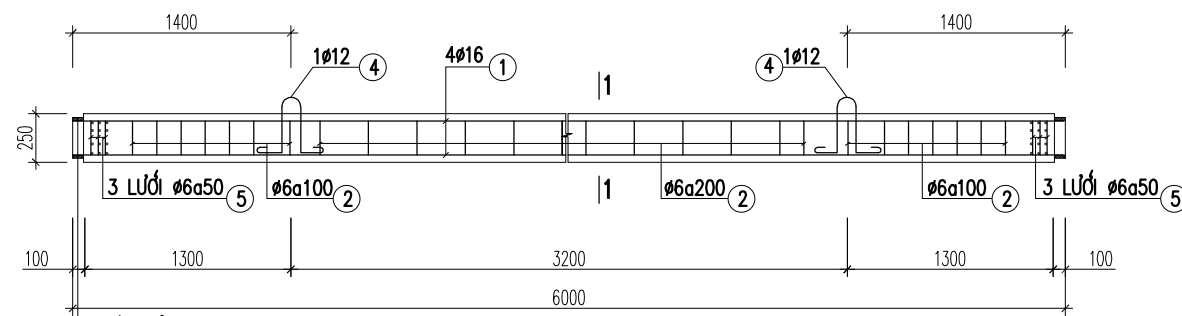


ĐOẠN CỌC THÂN C1 (1 ĐOẠN)

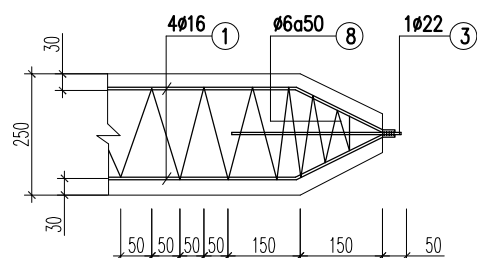


CHI TIẾT A

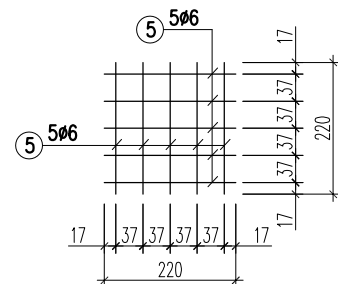


LƯỚI S1

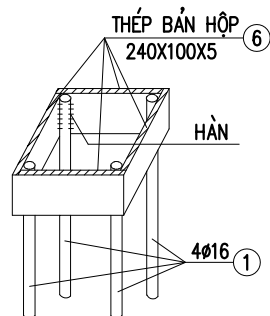


CHI TIẾT HÀN THÉP
BÀN ĐẦU CỌC

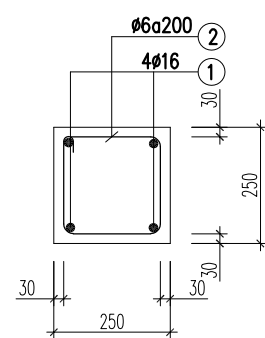


MẶT CẮT 1-1

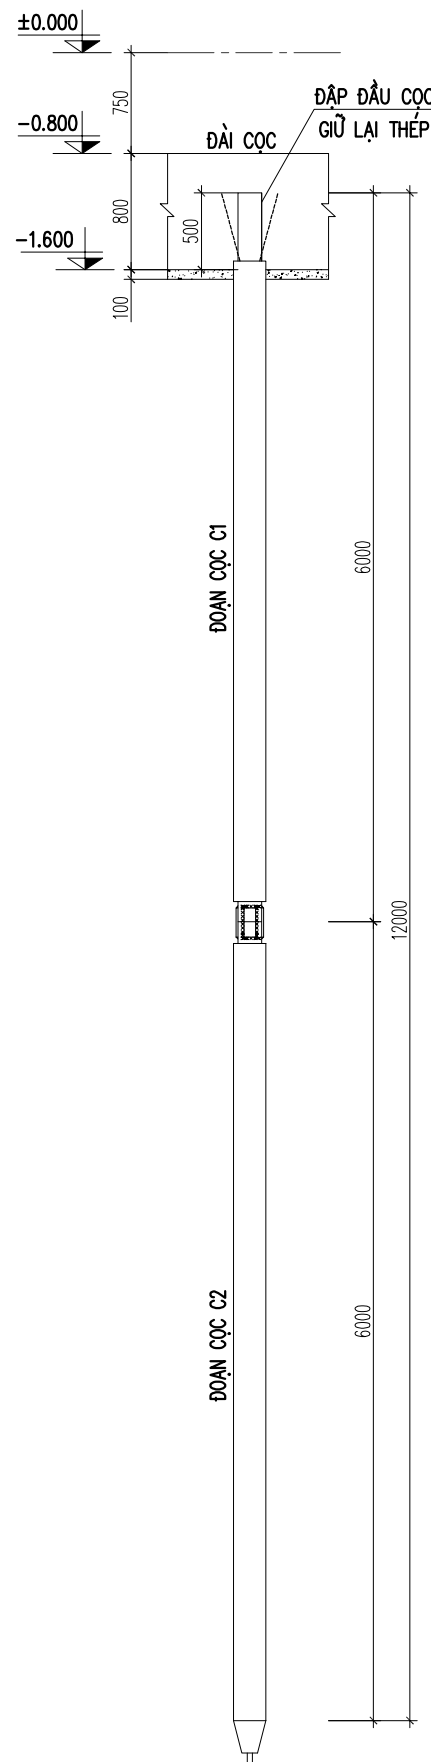

SƠ ĐỒ CỌC ĐẠI TRÀ

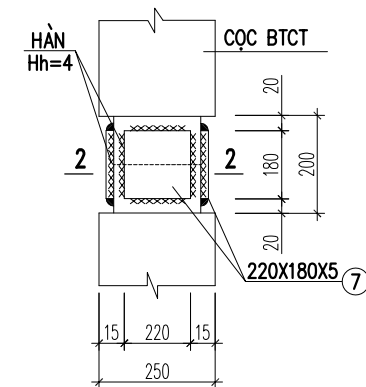

CHI TIẾT NỐI CỌC

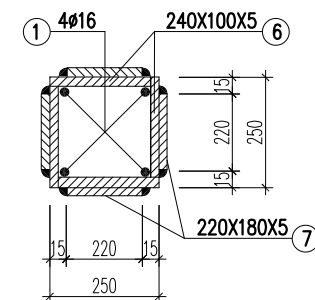

MẶT CẮT 2-2

GHI CHÚ:

- + BÊ TÔNG CỌC MÁC 250# BẢO DƯỠNG ĐÚNG QUY PHẠM KỸ THUẬT
- + KHI ĐẠT CƯỜNG ĐỘ 100% MỚI ĐƯỢC VẬN CHUYỂN THI CÔNG
- + THÉP AI ($\phi < 10$) CÓ $R_a = 2250 \text{ KG/M}^2$
- + THÉP AII ($\phi \geq 10$) CÓ $R_a = 2800 \text{ KG/M}^2$
- + THÉP TẤM, THÉP GÓC LOẠI CT3 CÓ $R = 2100 \text{ KG/M}^2$
- + QUE HÀN E42 HAY TƯƠNG ĐƯƠNG
- + SỬ DỤNG CỌC BÊ TÔNG CỐT THÉP TIẾT DIỆN $250 \times 250 \text{ MM}$
- + SỨC CHỊU TẢI THIẾT KẾ CỦA CỌC $[P] = 35 \text{ T}$
- + LỰC ÉP NHỎ NHẤT = 70 TẤN
- + LỰC ÉP LỚN NHẤT = 80 TẤN
- + TỔNG SỐ LƯỢNG CỌC ÉP ĐẠI TRÀ LÀ 70 CỌC. MỖI CỌC TẠM TÍNH DÀI 12.0M GỒM 1 ĐOẠN THÂN DÀI 6.0M VÀ 1 ĐOẠN MŨI DÀI 6.0M
- + KHI CÓ KẾT QUẢ ÉP THÍ NGHIỆM CỌC MỚI ĐƯỢC ÉP CỌC ĐẠI TRÀ
- + CHIỀU DÀI CỌC CÓ THỂ THAY ĐỔI SAU KHI CÓ KẾT QUẢ ÉP THỬ CỌC
- + KHI THI CÔNG ĐÀM CẦN ĐẬP VỠ ĐẦU CỌC 40CM (LÀM SẠCH ĐẦU CỌC VÀ THÉP) ĐỂ LIÊN KẾT CỌC VỚI ĐÀM
- + KHI TRIỂN KHAI THI CÔNG, ĐƠN VỊ THI CÔNG VÀ TỰ VẤN GIÁM SÁT CẦN THEO DÕI QUÁ TRÌNH ÉP CỌC VÀ PHẢI CẤP SỐ LIỆU LỰC ÉP TRÊN MÁY CHO TỰ VẤN THIẾT KẾ BIẾT ĐỂ CÓ BIỆN PHÁP ĐIỀU CHỈNH MÓNG

CHỦ ĐẦU TƯ

ANH SỸ

CÔNG TRÌNH

KHÁCH SẠN

ĐỊA ĐIỂM

YÊN LỆNH, THÁI THUY, HUNG YÊN

ĐƠN VỊ THIẾT KẾ



CÔNG TY CỔ PHẦN
TƯ VẤN THIẾT KẾ HÀ NỘI

ĐC: SN71 SƠN ĐỒNG, HÀ NỘI
TEL: 0983.381.930

GIÁM ĐỐC

NGUYỄN ĐỨC MINH

CHỦ TRÌ DỰ ÁN

KTS. NGUYỄN ĐỨC MINH

THIẾT KẾ

KTS. NGUYỄN ĐOÀN HIẾU

KẾT CẤU

KS. TRẦN VĂN ANH

GIAI ĐOẠN

H.S.X.P

HẠNG MỤC

KIẾN TRÚC

TÊN BẢN VẼ


CHI TIẾT CỌC

HOÀN THÀNH

02/2026

KÝ HIỆU BẢN VẼ

KC-01

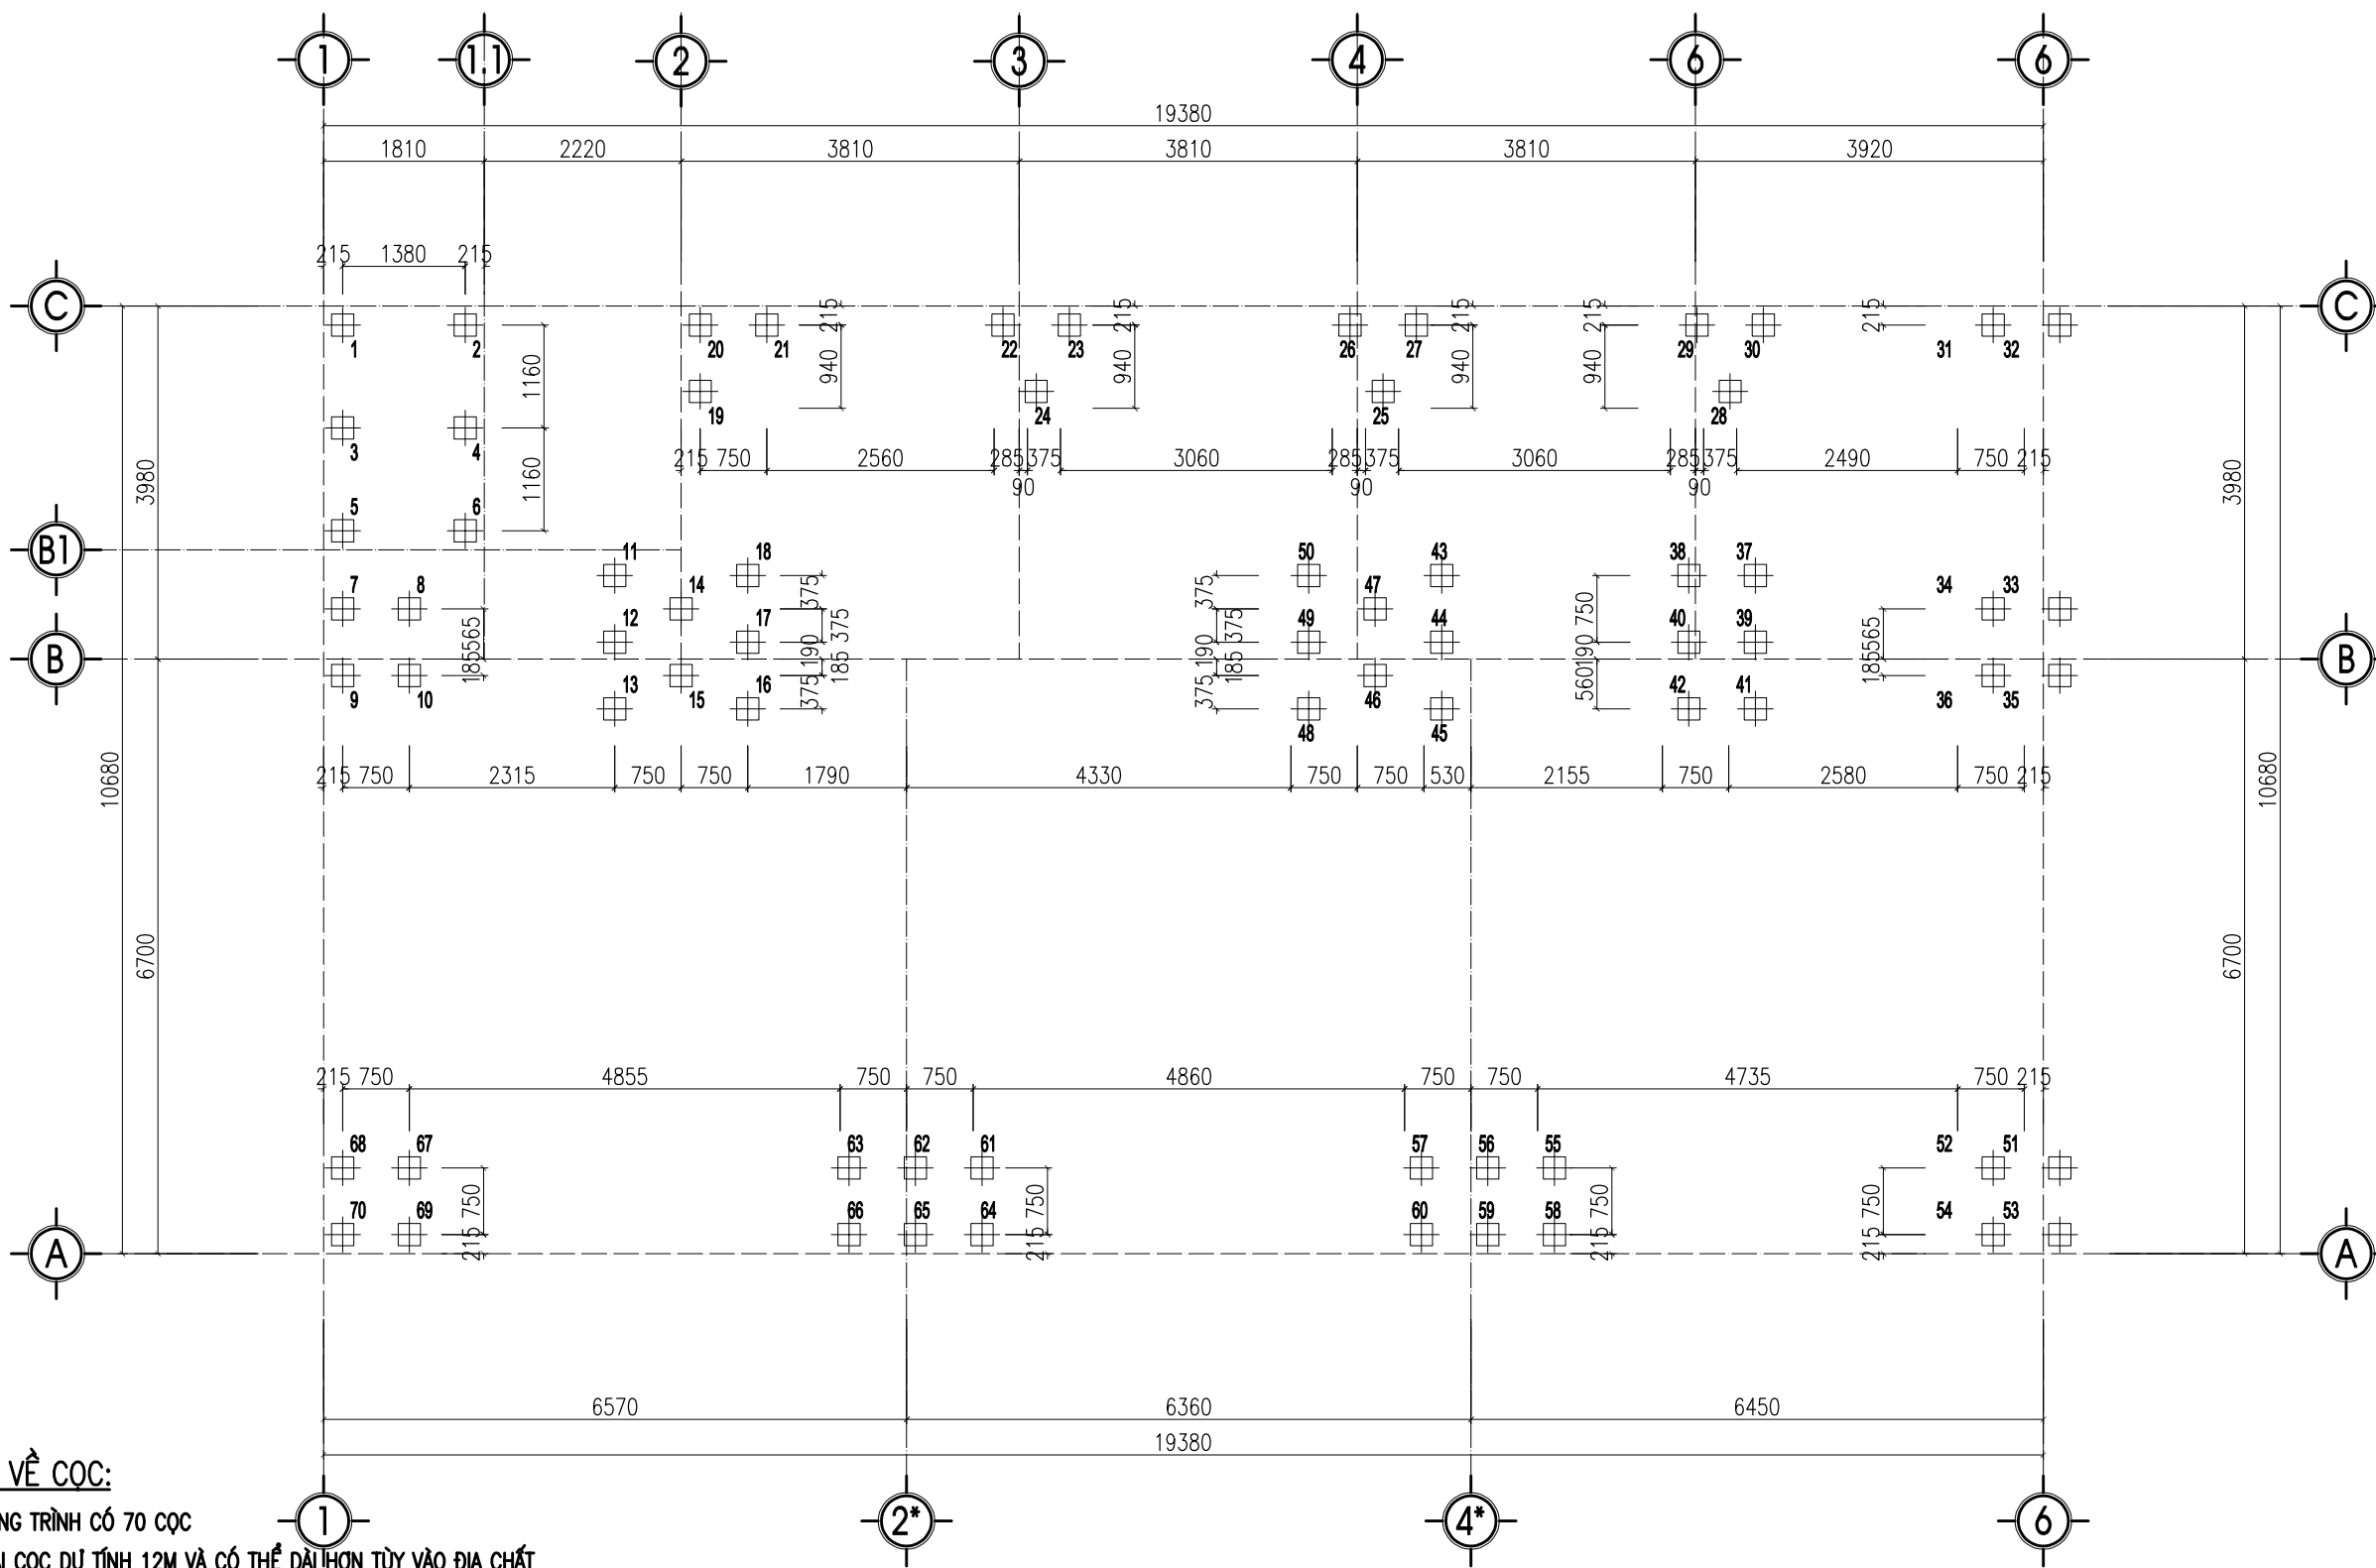

GHI CHÚ VỀ CỌC:

- TỔNG CÔNG TRÌNH CÓ 70 CỌC
- CHIỀU DÀI CỌC DỰ TÍNH 12M VÀ CÓ THỂ DÀI HƠN TÙY VÀO ĐỊA CHẤT
- CỌC SỬ DỤNG ĐƯỜNG KÍNH 250X250 CÓ PTK=35T, LỰC ÉP ĐẦU CỌC KHI THI CÔNG P_{MIN}=70T, P_{MAX}=80T
- CHỈ DÙNG ÉP CỌC KHI ĐỦ ĐỘ CHỐI. ĐẬP ĐẦU CỌC : 40CM
- VẬT LIỆU LÀM CỌC PHẢI ĐẢM BẢO ĐỂ CỌC KHÔNG BỊ PHÁ HOẠI KHI THI CÔNG:
 - + BÊTÔNG CỌC: CẤP BỀN B20 (MÁC 250#): R_B=11.5 MPA.
 - + CỐT THÉP CỌC: - THÉP CÓ ĐƯỜNG KÍNH $\phi < 10$, DÙNG THÉP CI, R_{SN}=235 MPA.
 - THÉP CÓ ĐƯỜNG KÍNH $\phi \geq 10$, DÙNG THÉP CI, R_{SN}=280 MPA.

MẶT BẰNG ĐỊNH VỊ CỌC

CHỦ ĐẦU TƯ

ANH SỸ

CÔNG TRÌNH

KHÁCH SẠN

ĐỊA ĐIỂM

YÊN LỆNH, THÁI THUY, HUNG YÊN

ĐƠN VỊ THIẾT KẾ



CÔNG TY CỔ PHẦN
TƯ VẤN THIẾT KẾ HÀ NỘI

ĐC: SN71 SƠN ĐỒNG, HÀ NỘI
TEL: 0983.381.930

GIÁM ĐỐC

(Signature)

NGUYỄN ĐỨC MINH

CHỦ TRÌ DỰ ÁN

(Signature)

KTS. NGUYỄN ĐỨC MINH

THIẾT KẾ

(Signature)

KTS. NGUYỄN DOÀN HIẾU

KẾT CẤU

(Signature)

KS. TRẦN VĂN ANH

GIAI ĐOẠN

H.S.X.P

HẠNG MỤC

KIẾN TRÚC

TÊN BẢN VẼ


MẶT BẰNG ĐỊNH VỊ CỌC

HOÀN THÀNH

02/2026

KÝ HIỆU BẢN VẼ

KC-02

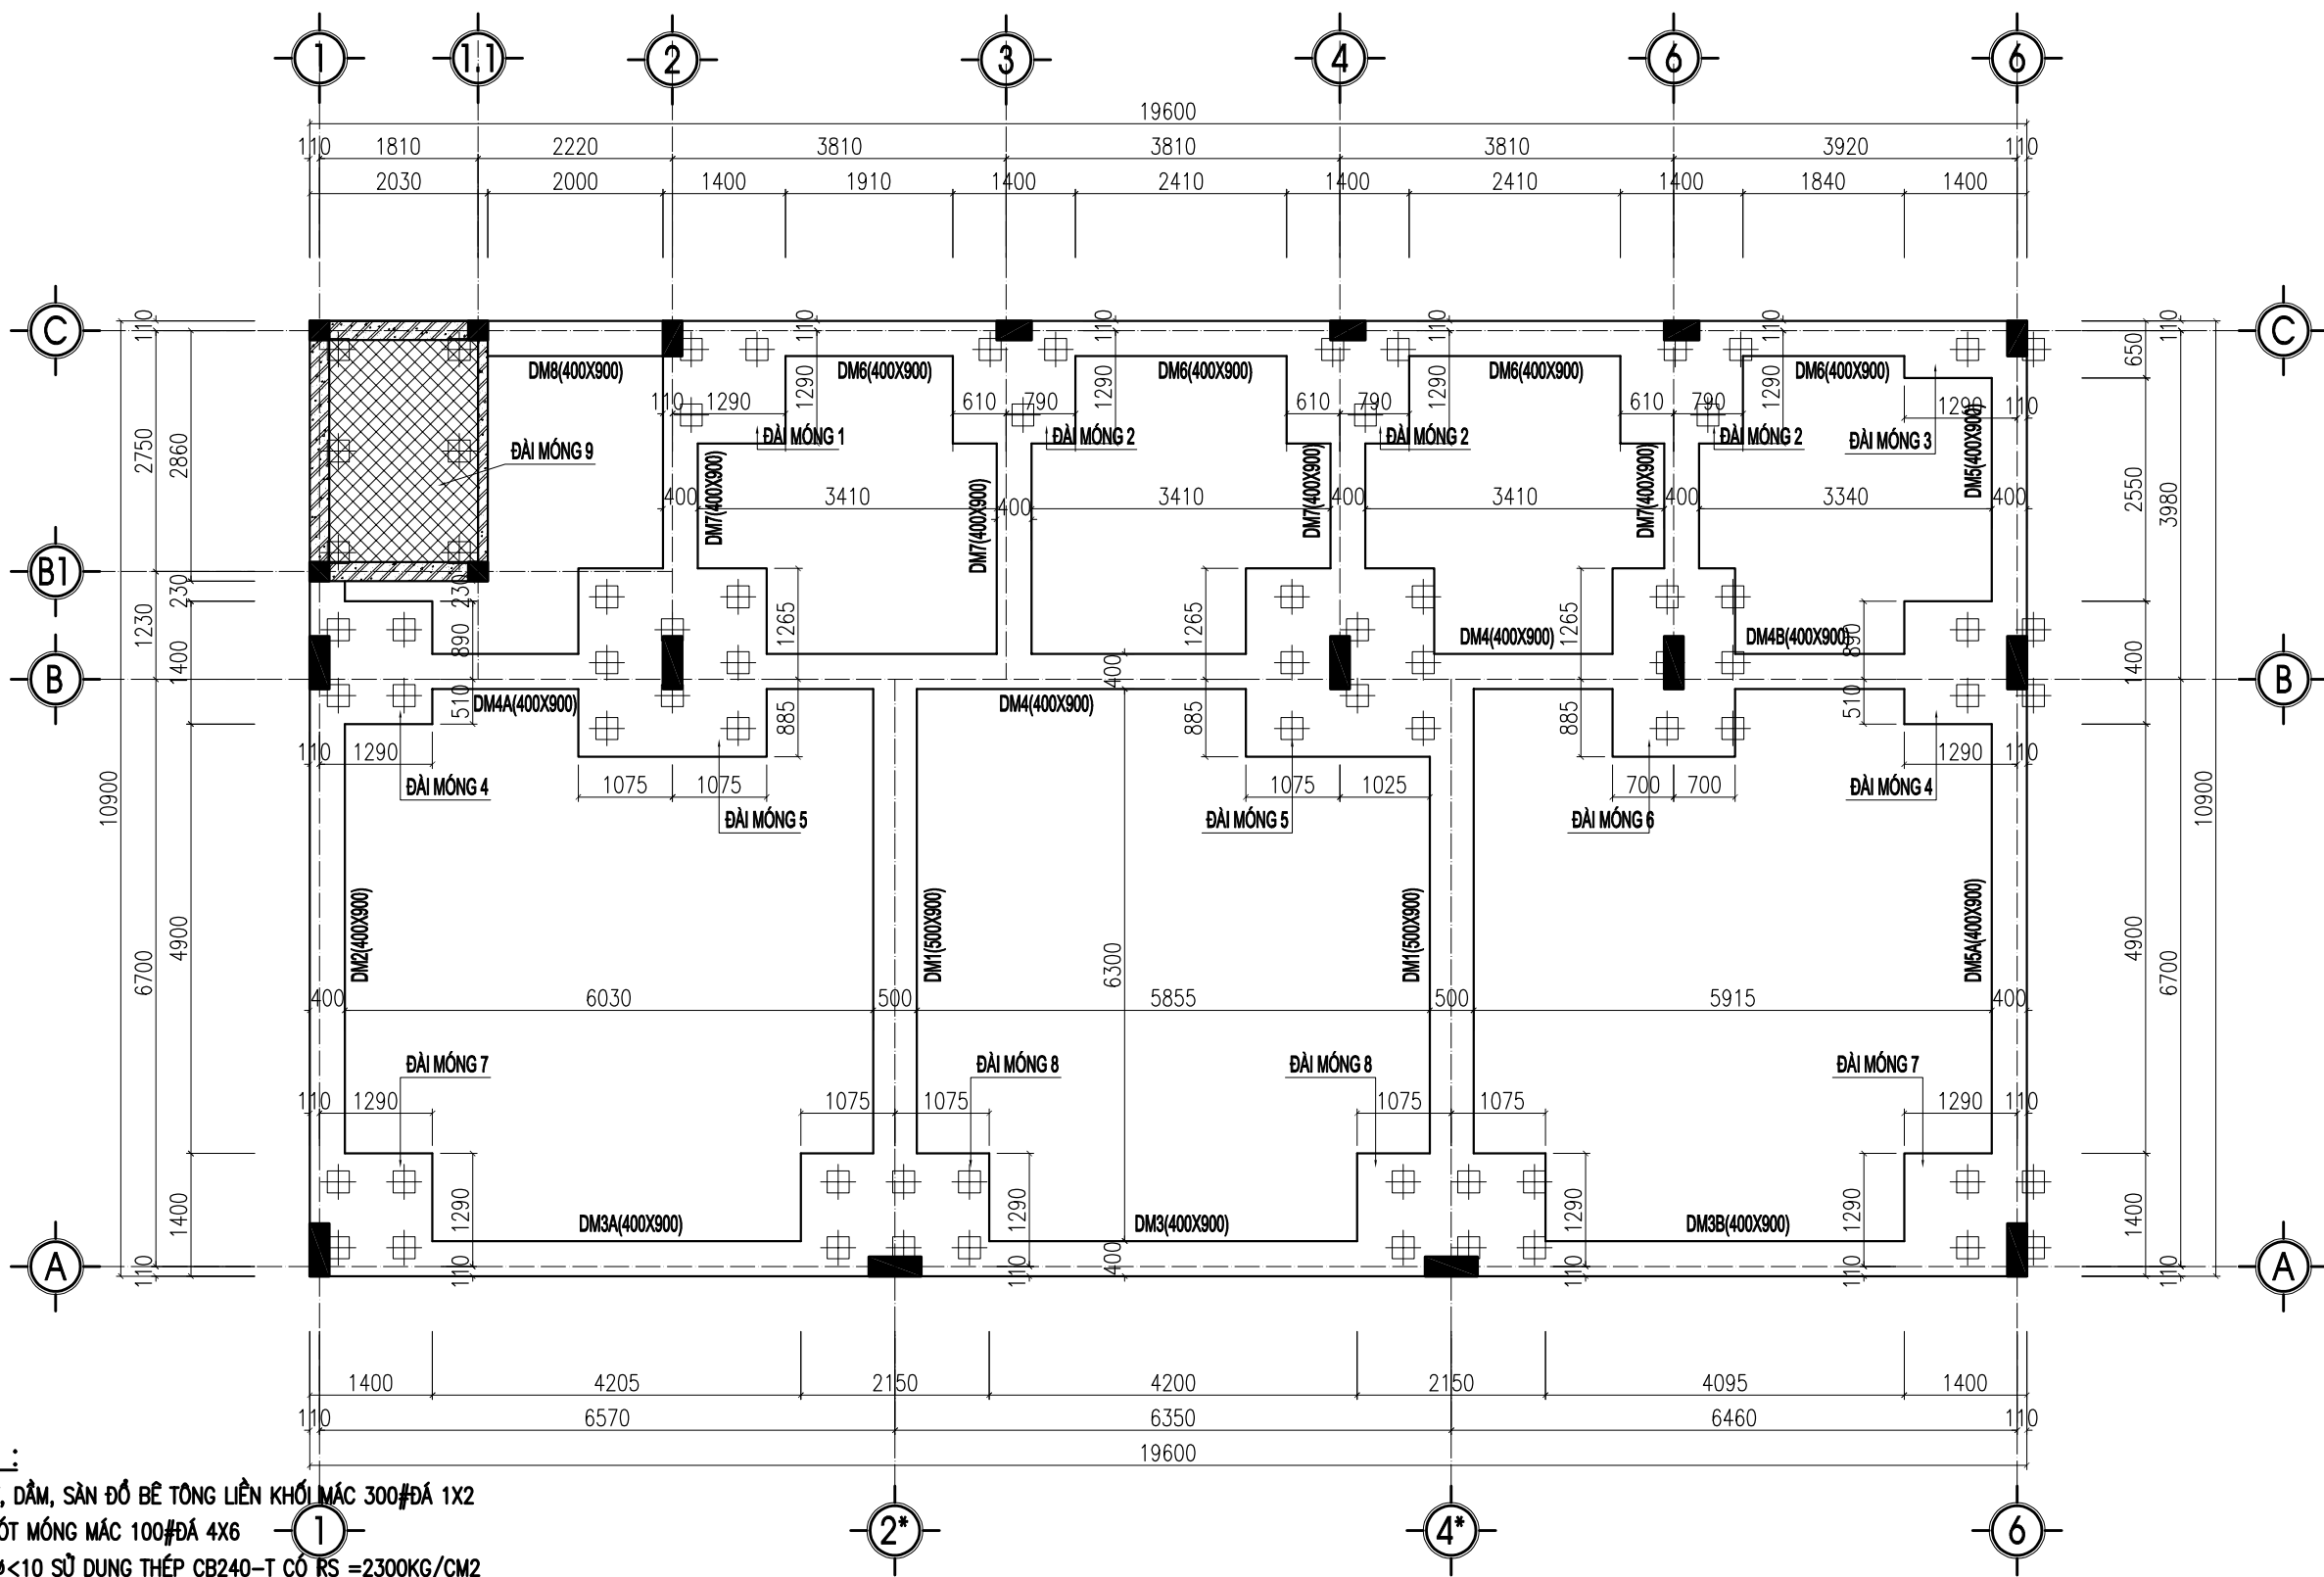

GHI CHÚ :

- MÓNG, CỘT, DẦM, SÀN ĐÓ BÊ TÔNG LIÊN KHỐI MÁC 300#ĐÁ 1X2
- BÊ TÔNG LÓT MÓNG MÁC 100#ĐÁ 4X6
- CỐT THÉP $\phi < 10$ SỬ DỤNG THÉP CB240-T CÓ RS =2300KG/CM2
- CỐT THÉP $\phi \geq 10$ SỬ DỤNG THÉP CB400-V CÓ RS =3650KG/CM2
- LỚP BÊ TÔNG BẢO VỆ MÓNG : 5CM
- LỚP BÊ TÔNG BẢO VỆ CỘT + VÁCH : 2,5CM
- CẮT, NỐI, UỐN THÉP ĐÚNG THEO QUY PHẠM
- TRƯỚC KHI CẮT THÉP CẦN KIỂM TRA LẠI KÍCH THƯỚC THỰC TẾ TẠI HIỆN TRƯỜNG
- KẾT HỢP XEM CÁC BẢN VẼ CÓ LIÊN QUAN

MẶT BẰNG KẾT CẤU MÓNG

VPDD: VĂN PHÒNG TƯ VẤN THIẾT KẾ NHÀ ĐẸP

ĐC: 390 - TRẦN HƯNG ĐẠO - TP.THÁI BÌNH

DESIGN: KIẾN TRÚC SƯ: NGUYỄN ĐỨC MINH

ĐD: 0983.381930

CHỦ ĐẦU TƯ

ANH SỸ

CÔNG TRÌNH

KHÁCH SẠN

ĐỊA ĐIỂM

YÊN LỆNH, THÁI THUY, HUNG YÊN

ĐƠN VỊ THIẾT KẾ



CÔNG TY CỔ PHẦN
TƯ VẤN THIẾT KẾ HÀ NỘI

ĐC: SN71 SƠN ĐỒNG, HÀ NỘI
TEL: 0983.381.930

GIÁM ĐỐC

(Signature)

NGUYỄN ĐỨC MINH

CHỦ TRÌ DỰ ÁN

(Signature)

KTS. NGUYỄN ĐỨC MINH

THIẾT KẾ

(Signature)

KTS. NGUYỄN DOÀN HIẾU

KẾT CẤU

(Signature)

KS. TRẦN VĂN ANH

GIẢI ĐOẠN

H.S.X.P

HẠNG MỤC

KIẾN TRÚC

TÊN BẢN VẼ


MẶT BẰNG KẾT CẤU MÓNG

HOÀN THÀNH

02/2026

KÝ HIỆU BẢN VẼ

KC-03

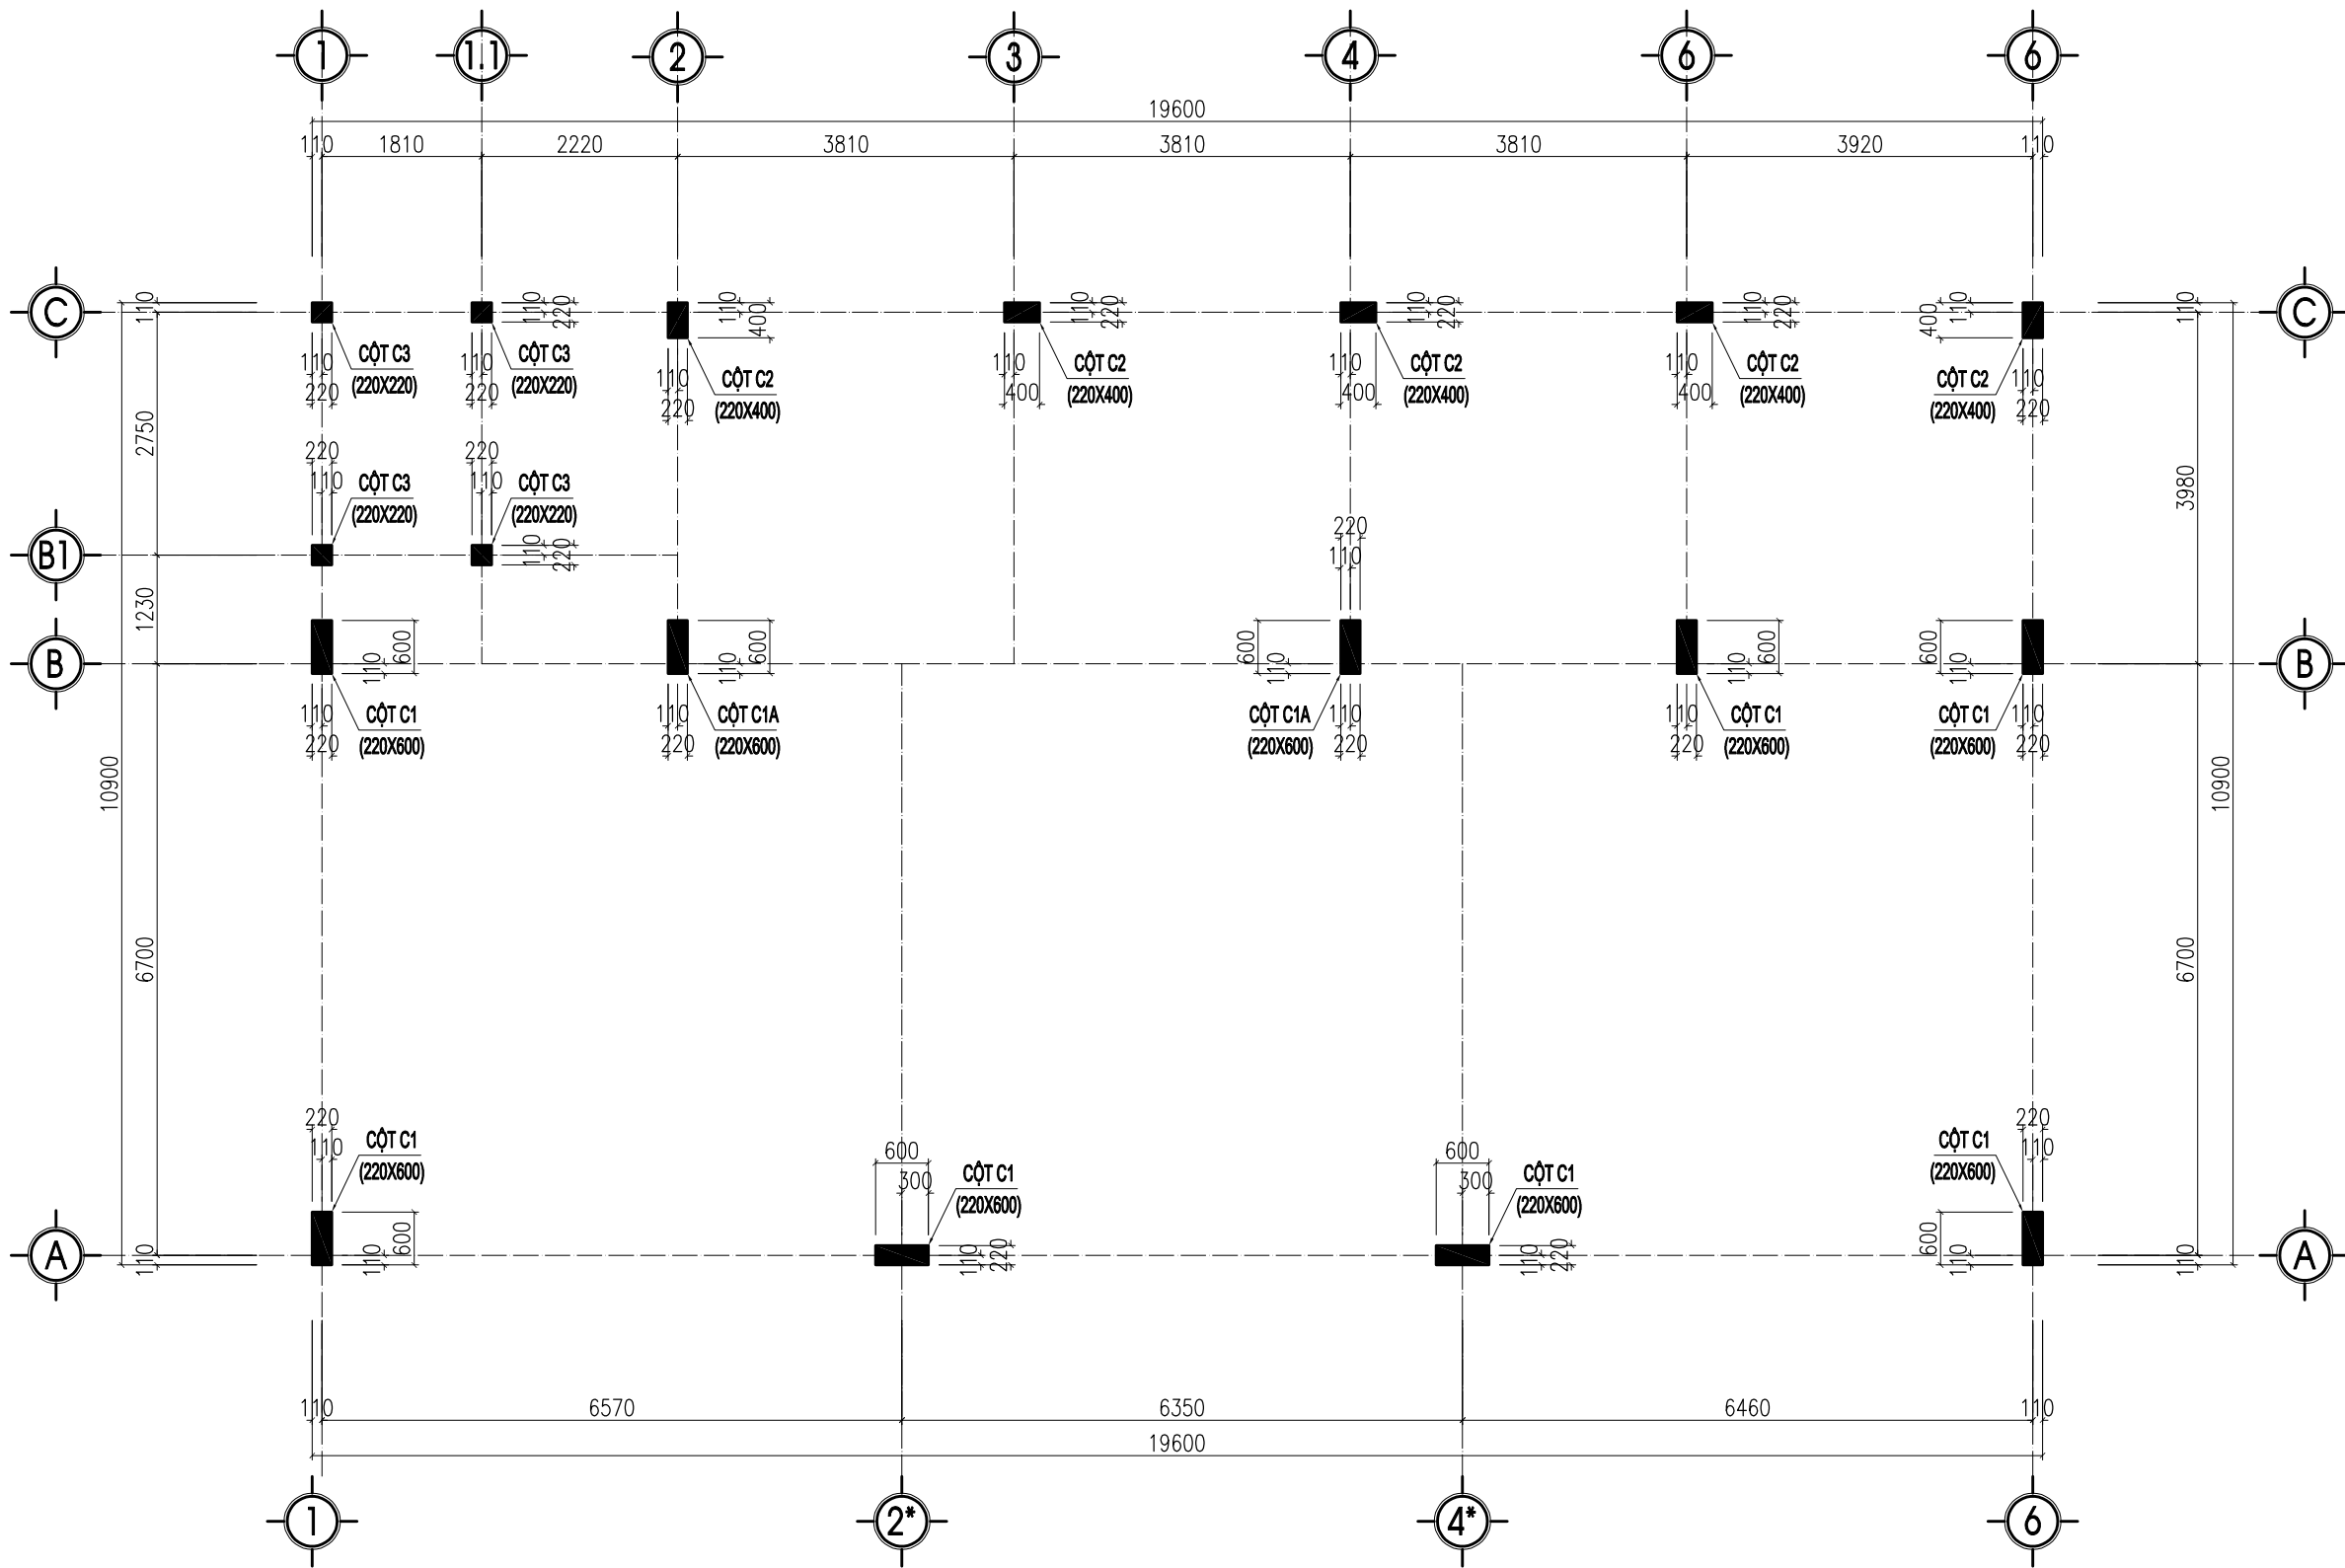

MẶT BẰNG ĐỊNH VỊ CỘT TẦNG 1

CHỦ ĐẦU TƯ

ANH SỸ

CÔNG TRÌNH

KHÁCH SẠN

ĐỊA ĐIỂM

YÊN LỆNH, THÁI THUY, HUNG YÊN

ĐƠN VỊ THIẾT KẾ



CÔNG TY CỔ PHẦN
TƯ VẤN THIẾT KẾ HÀ NỘI

ĐC: SN71 SƠN ĐỒNG, HÀ NỘI
TEL: 0983.381.930

GIÁM ĐỐC

NGUYỄN ĐỨC MINH

CHỦ TRÌ DỰ ÁN

KTS. NGUYỄN ĐỨC MINH

THIẾT KẾ

KTS. NGUYỄN ĐOÀN HIẾU

KẾT CẤU

KS. TRẦN VĂN ANH

GIAI ĐOẠN

H.S.X.P

HẠNG MỤC

KIẾN TRÚC

TÊN BẢN VẼ


MẶT BẰNG ĐỊNH VỊ CỘT TẦNG 1

HOÀN THÀNH

02/2026

KÝ HIỆU BẢN VẼ

KC-04

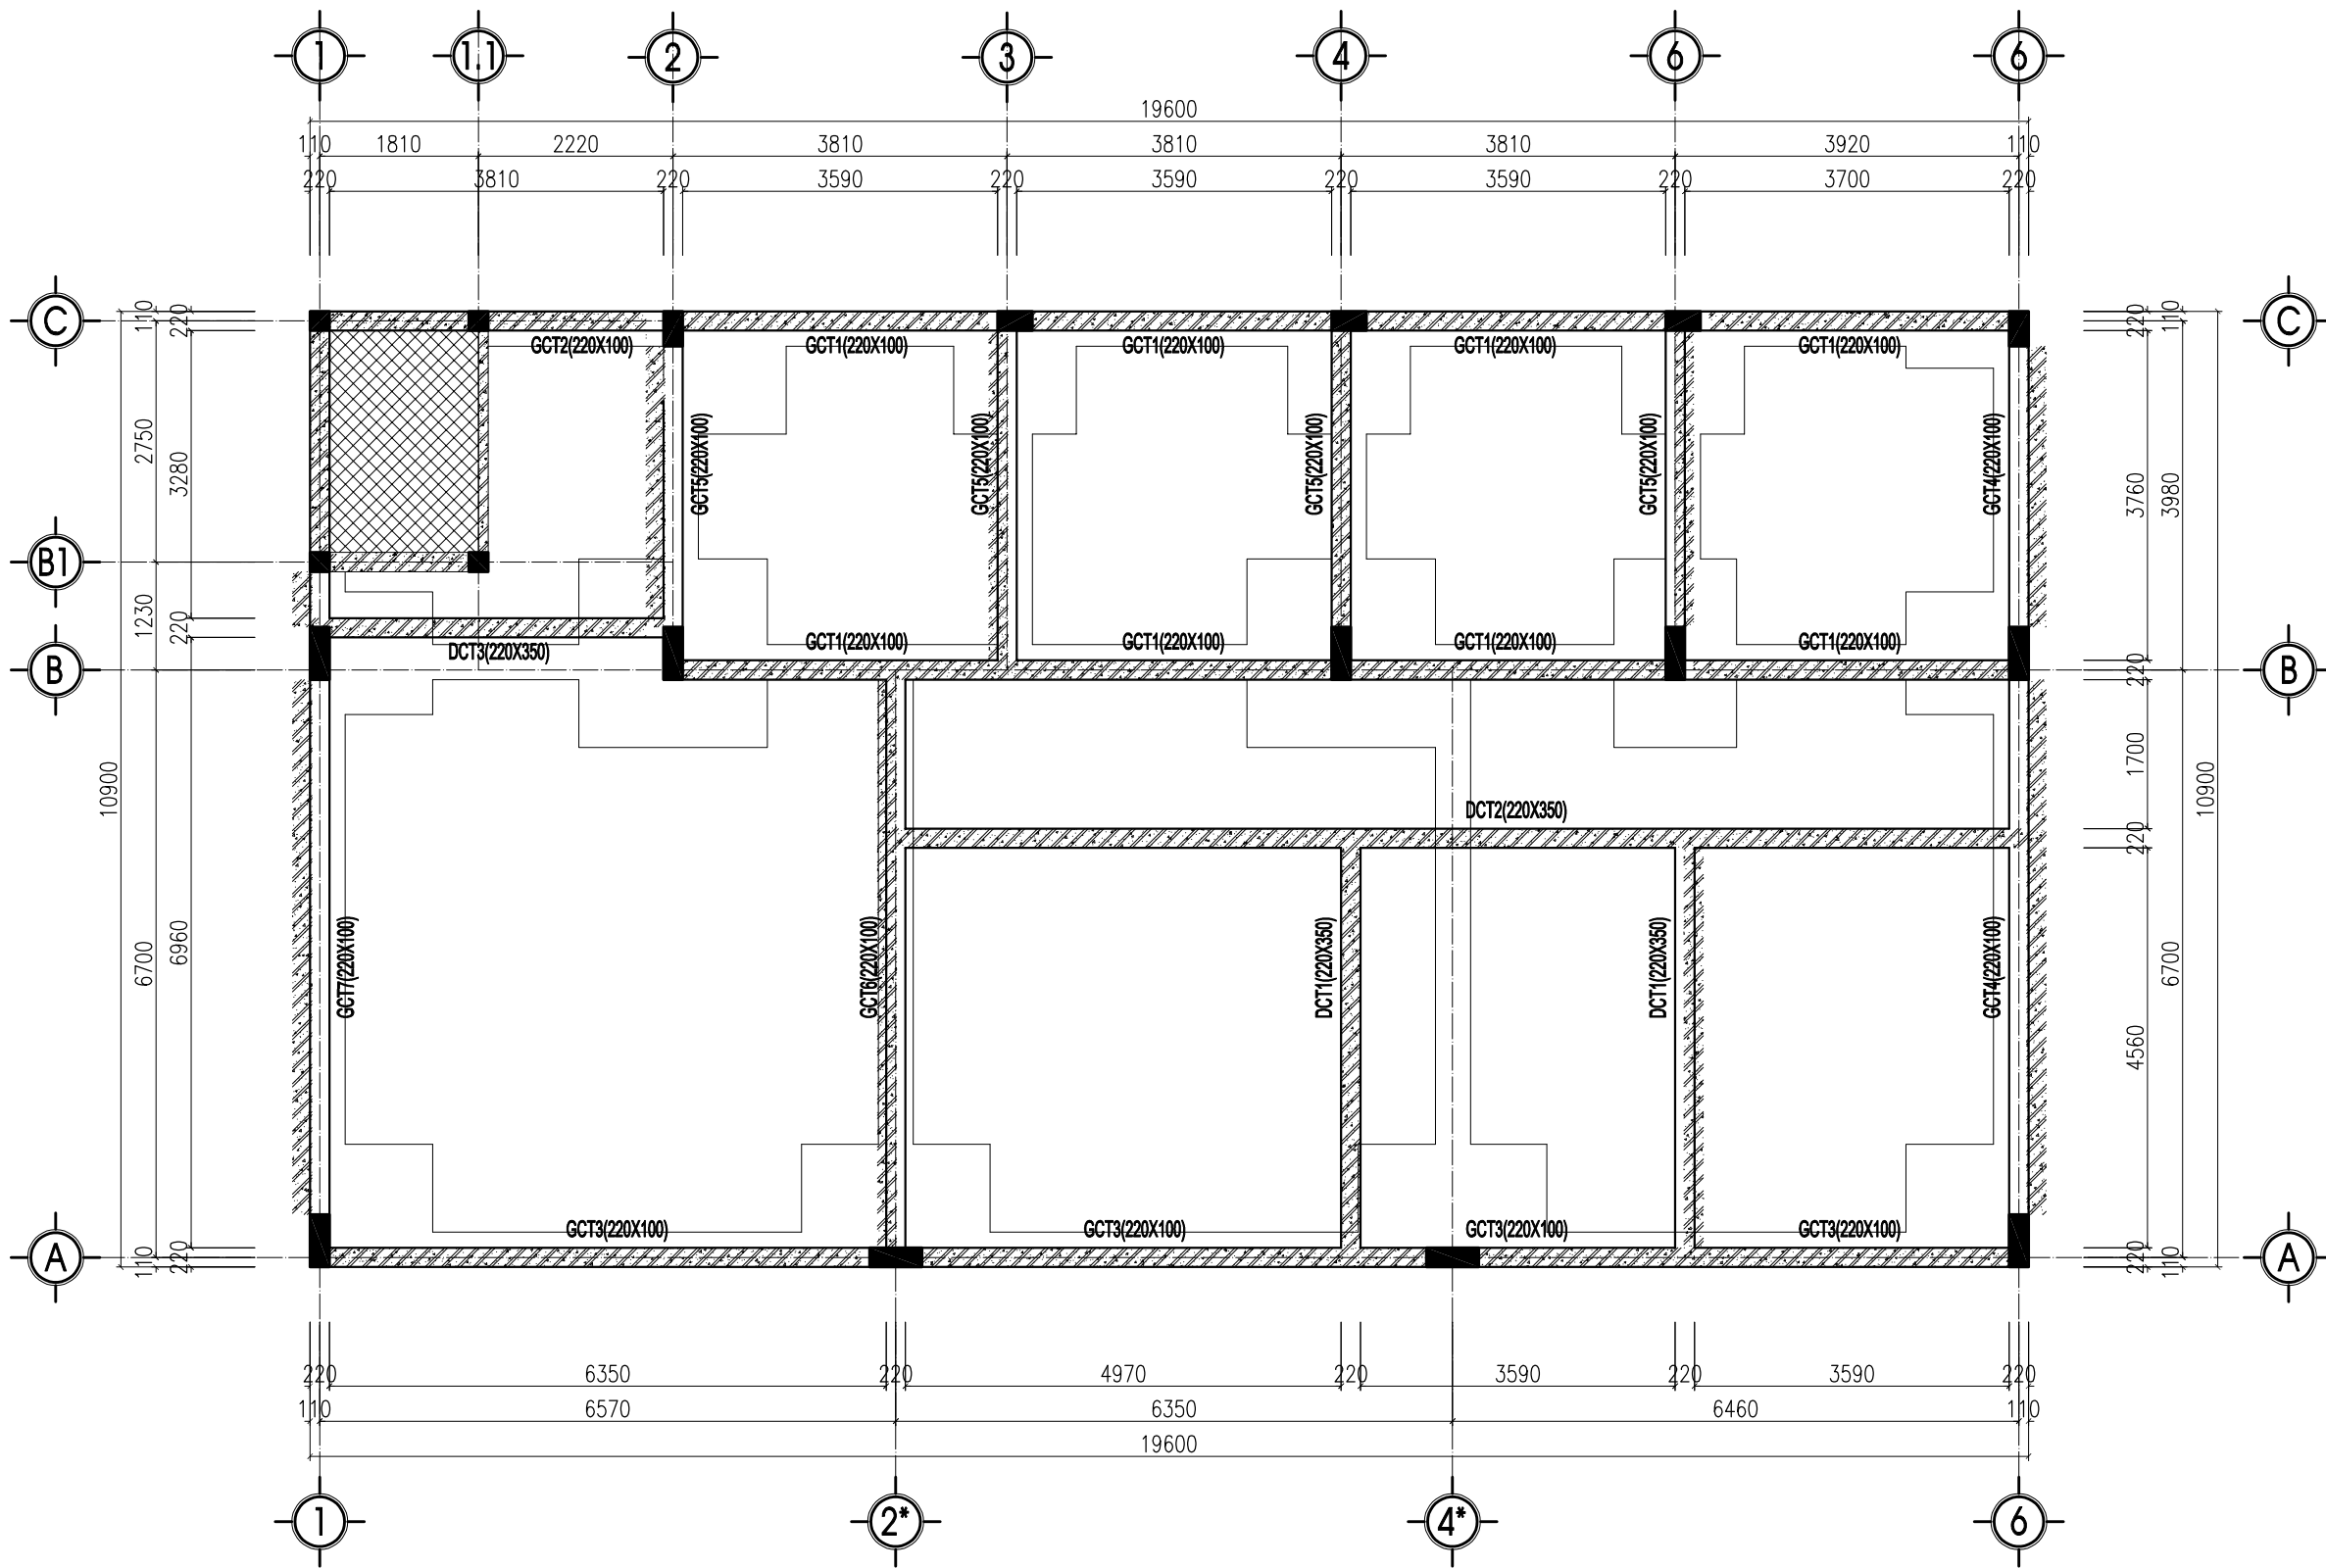

MẶT BẰNG GIẢNG CHÂN TƯỜNG + DẦM CHÂN TƯỜNG

CHỦ ĐẦU TƯ

ANH SỸ

CÔNG TRÌNH

KHÁCH SẠN

ĐỊA ĐIỂM

YÊN LỆNH, THÁI THỤY, HUNG YÊN

ĐƠN VỊ THIẾT KẾ



CÔNG TY CỔ PHẦN
TƯ VẤN THIẾT KẾ HÀ NỘI

ĐC: SN71 SƠN ĐỒNG, HÀ NỘI
TEL: 0983.381.930

GIÁM ĐỐC

NGUYỄN ĐỨC MINH

CHỦ TRÌ DỰ ÁN

KTS. NGUYỄN ĐỨC MINH

THIẾT KẾ

KTS. NGUYỄN ĐOÀN HIẾU

KẾT CẤU

KS. TRẦN VĂN ANH

GIAI ĐOẠN

H.S.X.P

HẠNG MỤC

KIẾN TRÚC

TÊN BẢN VẼ


MẶT BẰNG GIẢNG CHÂN TƯỜNG
+ DẦM CHÂN TƯỜNG

HOÀN THÀNH

02/2026

KÝ HIỆU BẢN VẼ

KC-05

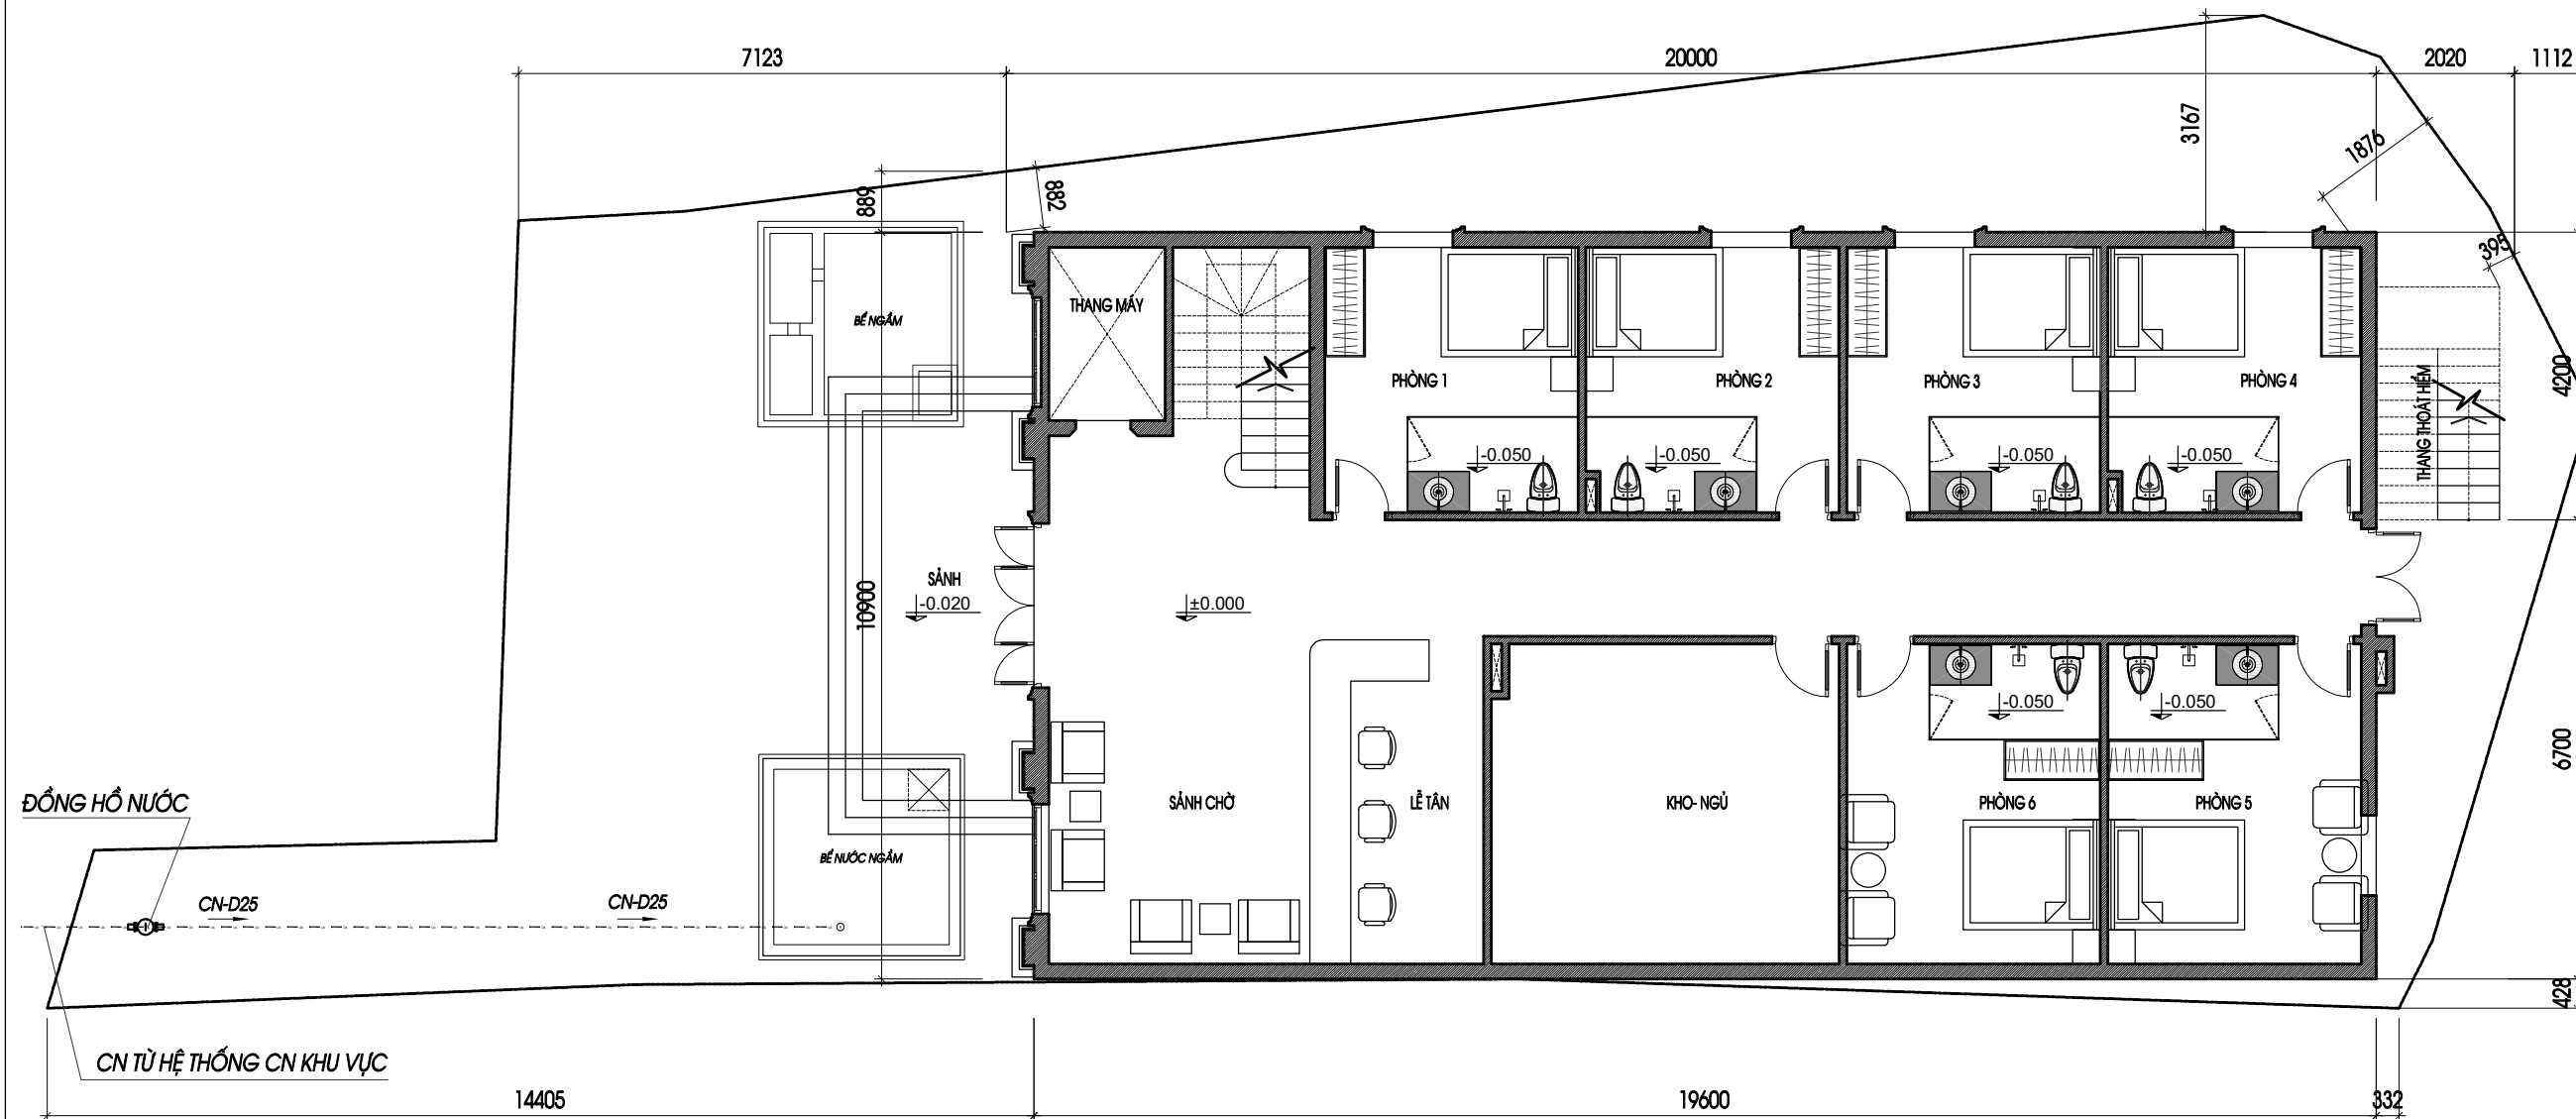

MẶT BẰNG CẤP THOÁT NƯỚC

VPDD: VĂN PHÒNG TƯ VẤN THIẾT KẾ NHÀ ĐẸP

ĐC: 390 - TRẦN HUNG ĐẠO - TP.THÁI BÌNH

DESIGN: KIẾN TRÚC SƯ: NGUYỄN ĐỨC MINH

ĐD: 0983.381930

CHỦ ĐẦU TƯ

ANH SỸ

CÔNG TRÌNH

KHÁCH SẠN

ĐỊA ĐIỂM

YÊN LỆNH, THÁI THUY, HUNG YÊN

ĐƠN VỊ THIẾT KẾ



CÔNG TY CỔ PHẦN
TƯ VẤN THIẾT KẾ HÀ NỘI

ĐC: SN71 SƠN ĐỒNG, HÀ NỘI
TEL: 0983.381.930

GIÁM ĐỐC

(Signature)

NGUYỄN ĐỨC MINH

CHỦ TRÌ DỰ ÁN

(Signature)

KTS. NGUYỄN ĐỨC MINH

THIẾT KẾ

(Signature)

KTS. NGUYỄN DOÀN HIẾU

KẾT CẤU

(Signature)

KS. TRẦN VĂN ANH

GIẢI ĐOẠN

H.S.X.P

HẠNG MỤC

KIẾN TRÚC

TÊN BẢN VẼ

MẶT BẰNG CẤP THOÁT NƯỚC

HOÀN THÀNH

02/2026

KÝ HIỆU BẢN VẼ

CTN-01